

APPROVAL DRAWINGS & RENDERS



PROJECT: 3-Bedroom Bungalow

CLIENT: Ms. Linda

the **KISERIAN HOUSE**

NOTES


CLIENT

Ms. Linda Munyendo

Location: Kiserian, Kajiado

Plot Number: Kajiado/ OLCHORO onyore/ 34169

ORIENTATION

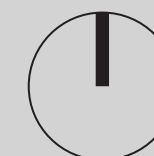

SCALE

1:1000

Location Plan

A3.01



the **KISERIAN HOUSE**

NOTES

CLIENT

Ms. Linda Munyendo

Location: Kiserian, Kajiado

Plot Number: Kajiado/ OLCHORO onyore/ 34169

ORIENTATION




SCALE

1:200

Site Plan

A3.02

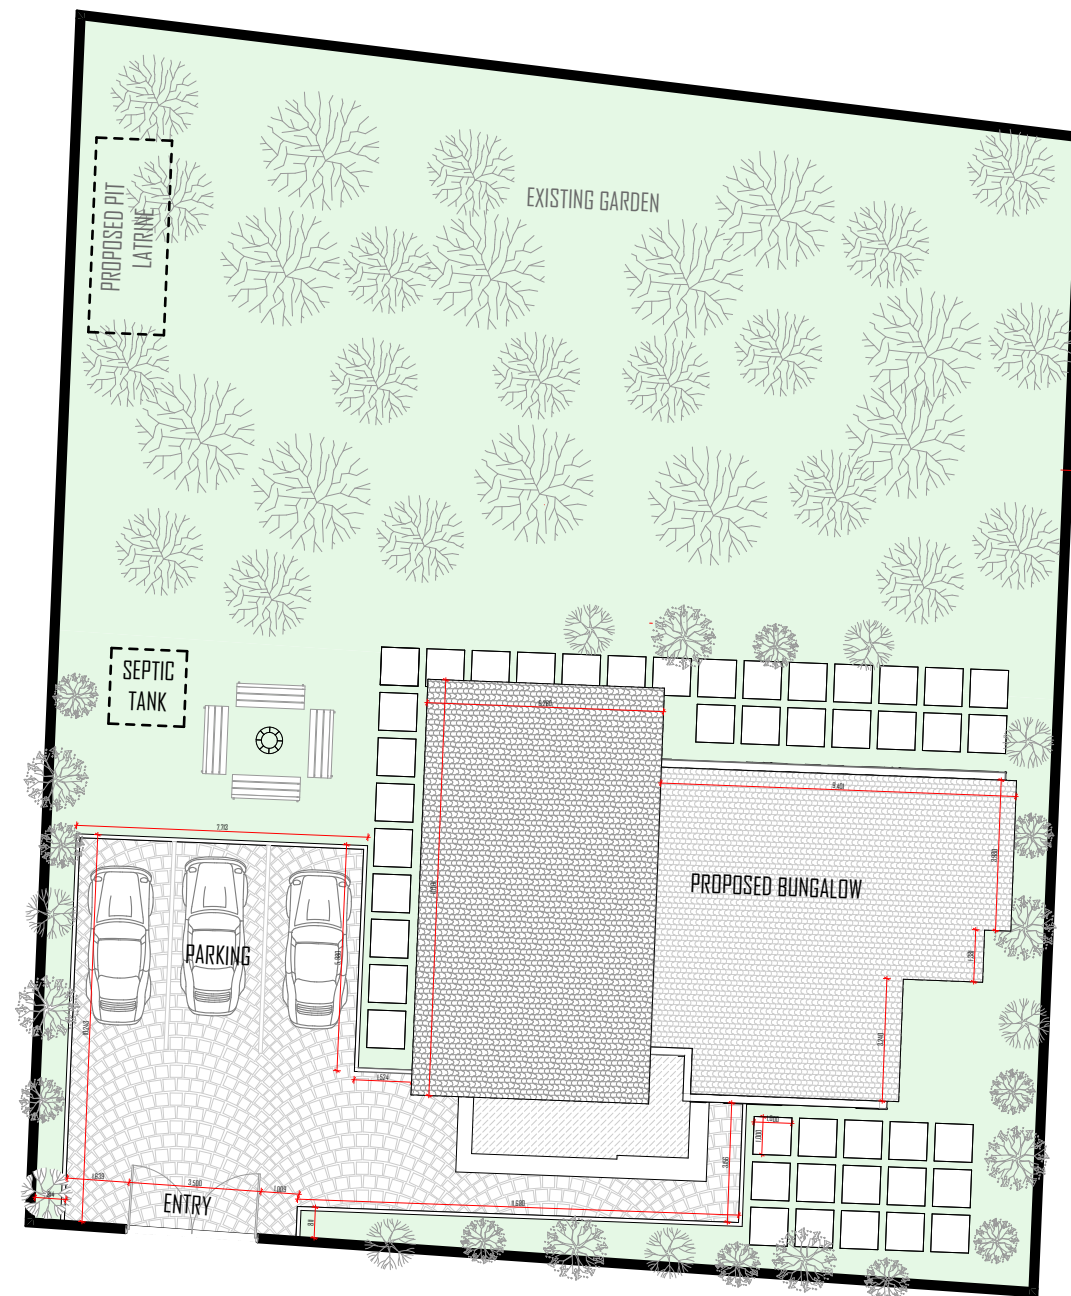

the **KISERIAN HOUSE**

NOTES

CLIENT

Ms. Linda Munyendo

Location: Kiserian, Kajiado

Plot Number: Kajiado/ OLCHORO onyore/ 34169

ORIENTATION




SCALE

1:100

Floor Plan

A3.03

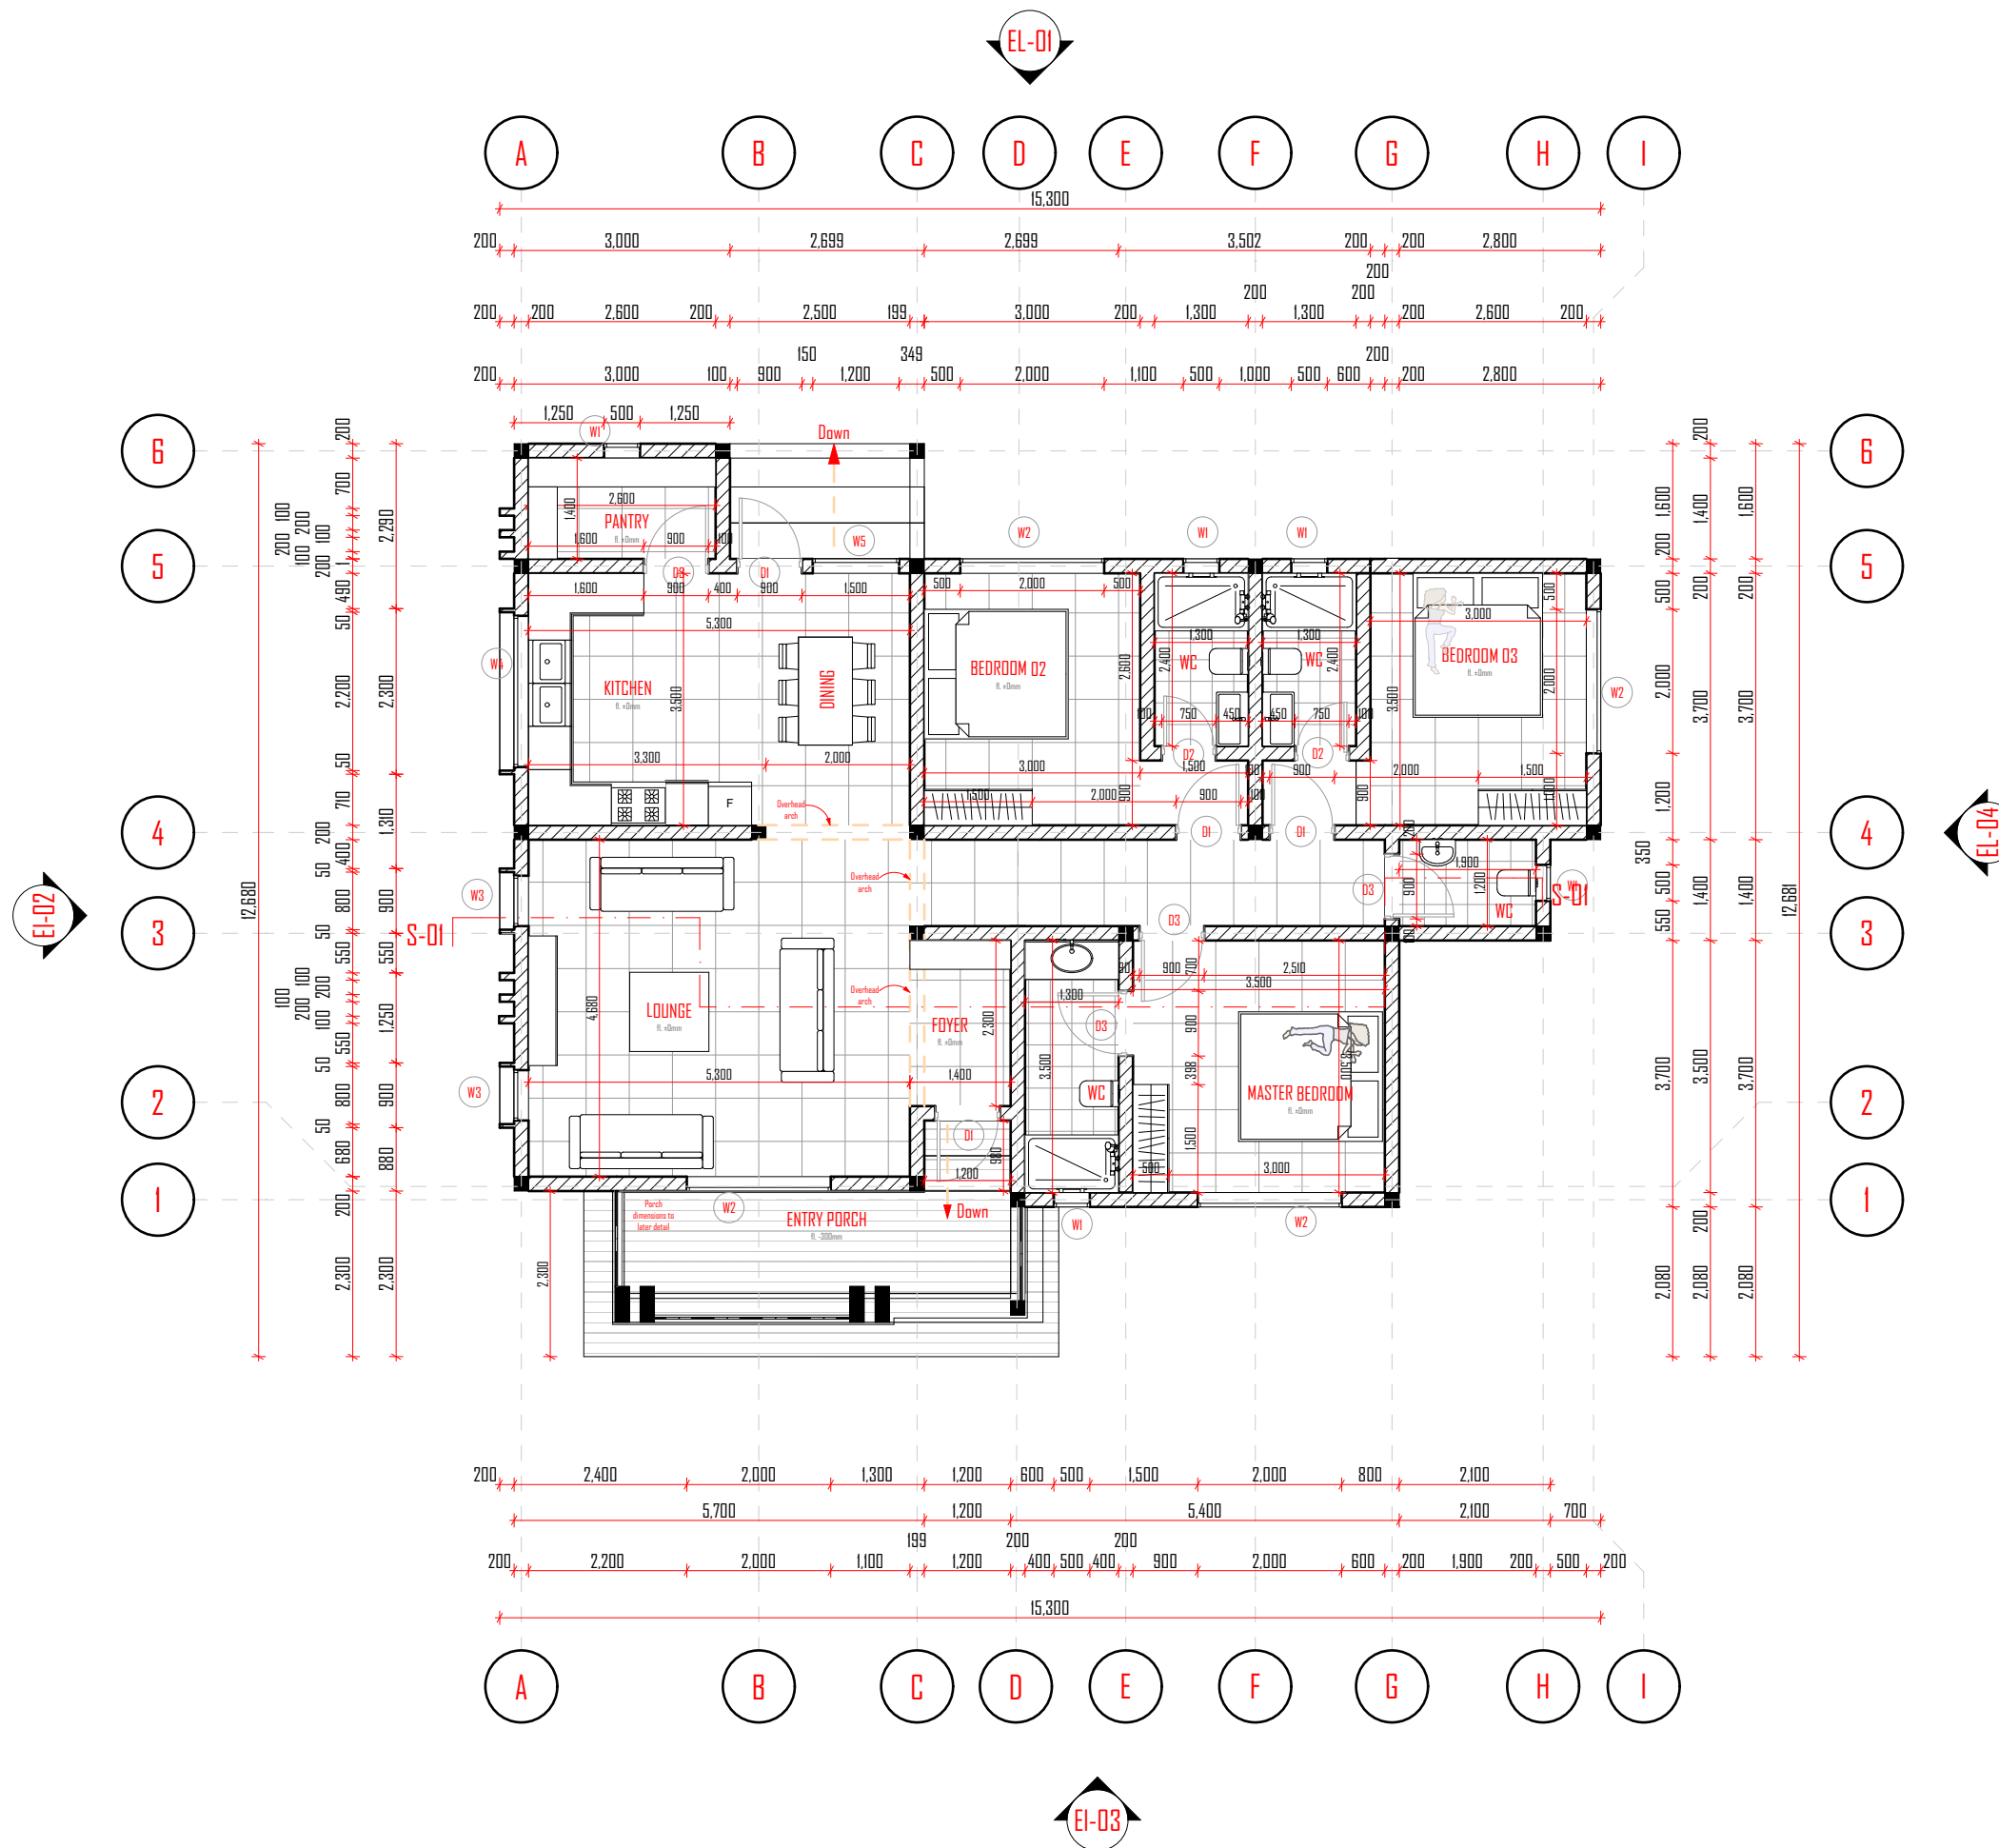

the **KISERIAN HOUSE**

NOTES

CLIENT

Ms. Linda Munyendo

Location: Kiserian, Kajiado

Plot Number: Kajiado/ OLCHORO onyore/ 34169

ORIENTATION




SCALE

1:100

Room Areas

A3.04

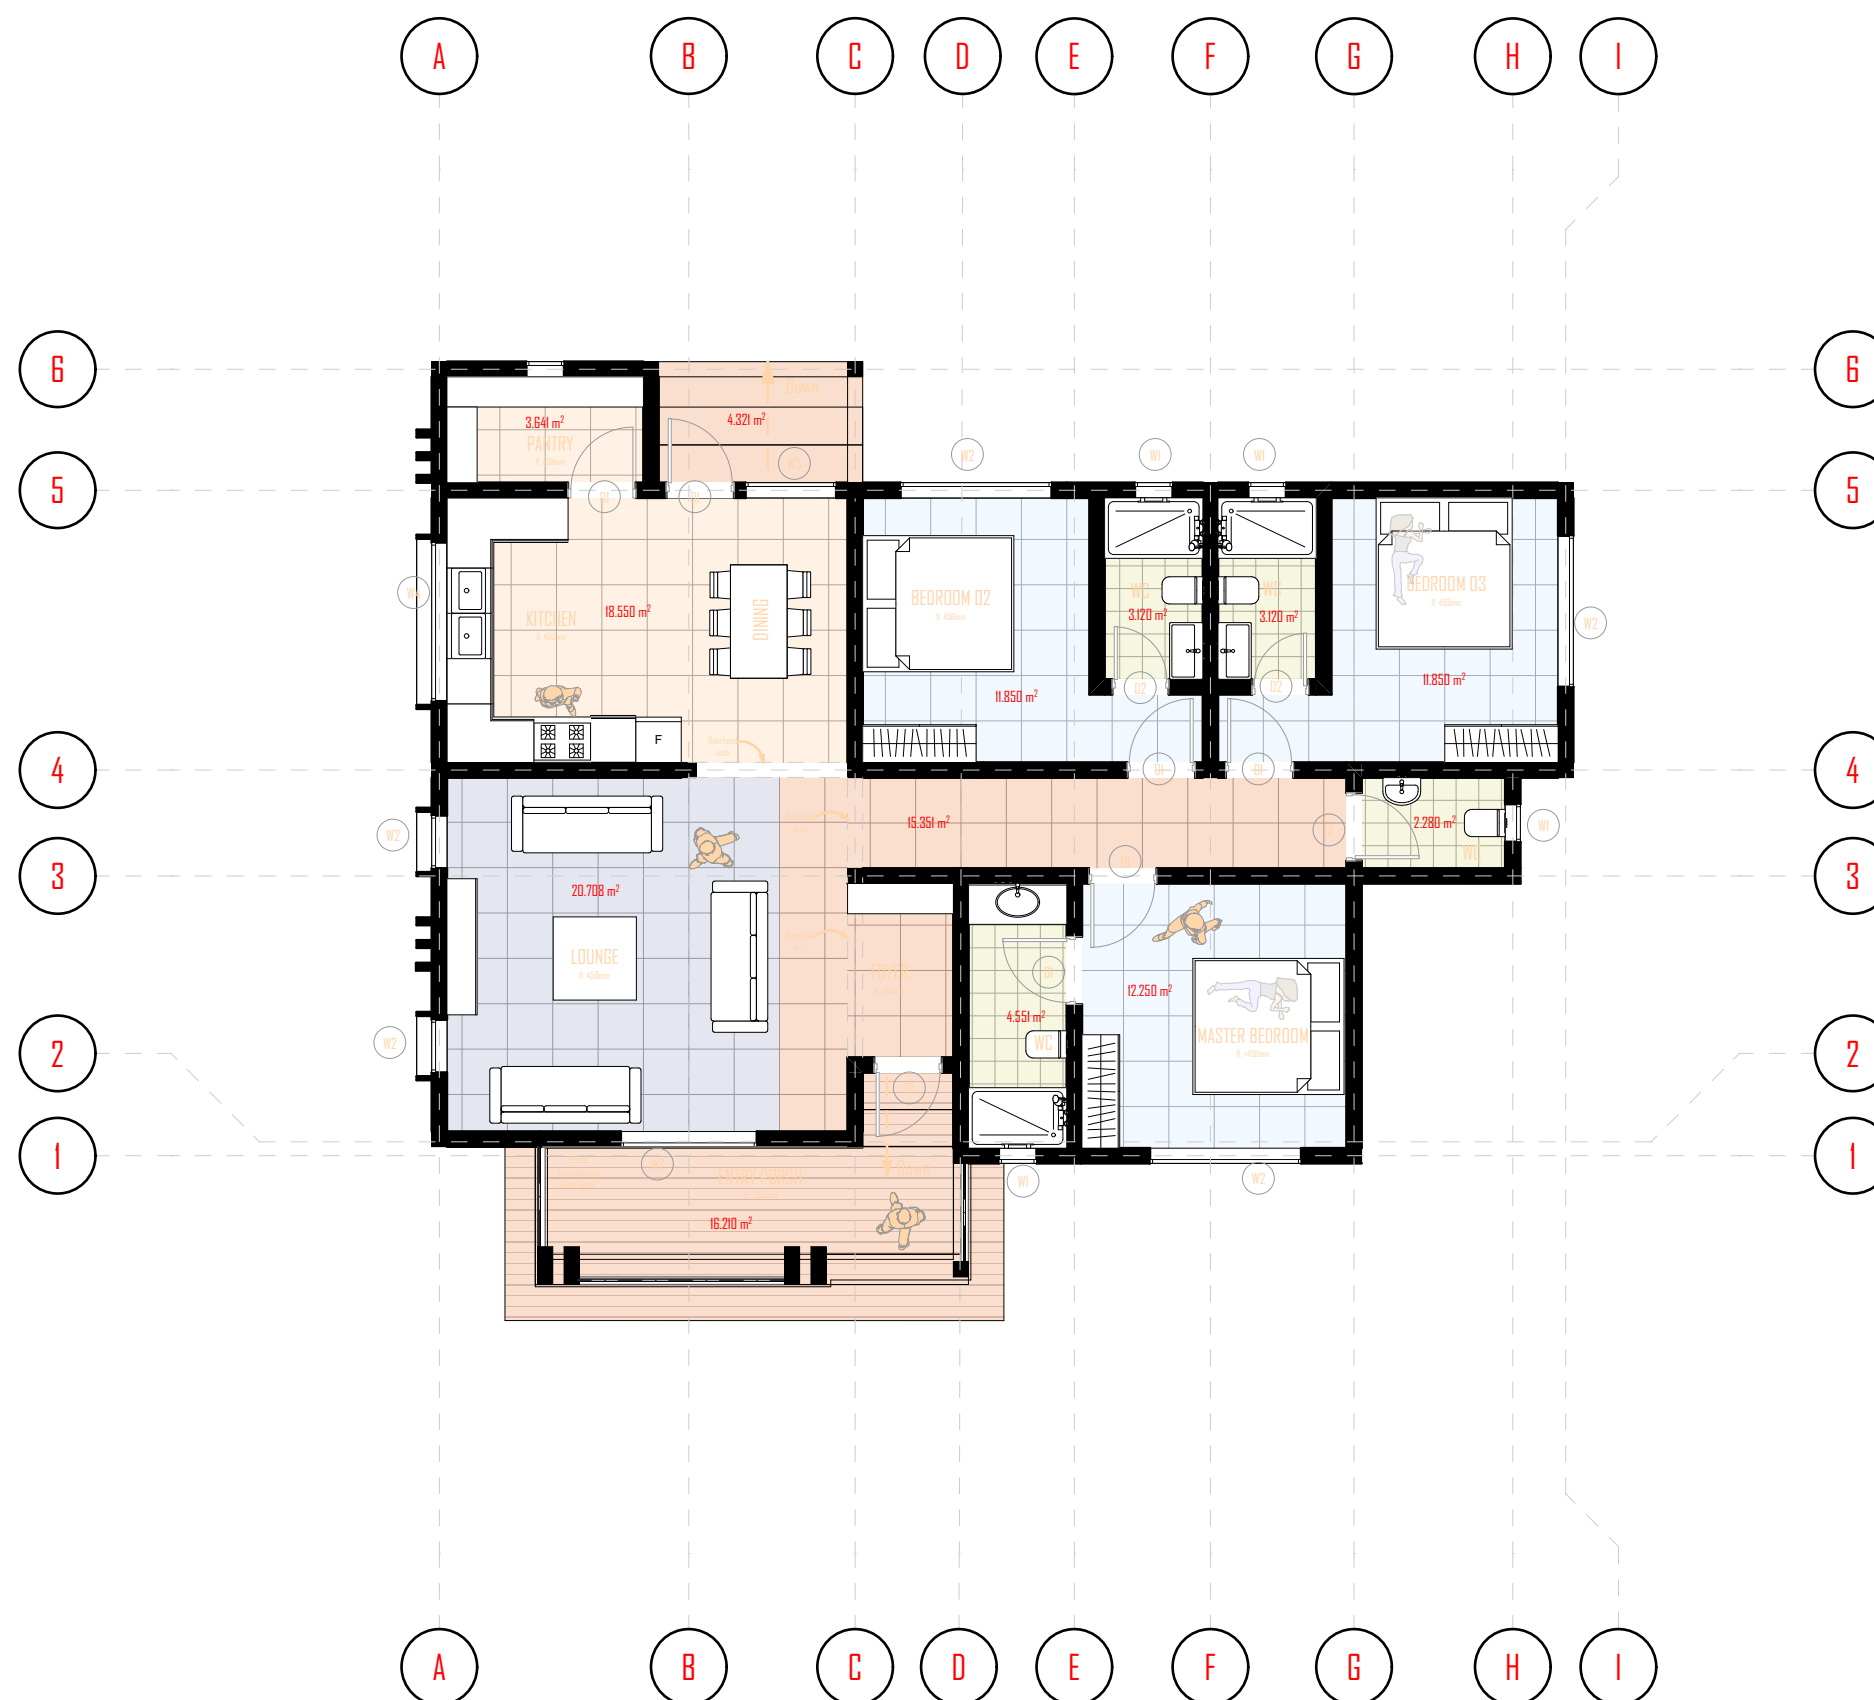

the **KISERIAN HOUSE**

NOTES


CLIENT

Ms. Linda Munyendo

Location: Kiserian, Kajiado

Plot Number: Kajiado/ OLCHORO onyore/ 34169

ORIENTATION

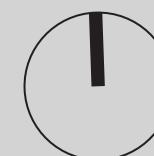


SCALE

1:100

Foundation Plan

A3.05

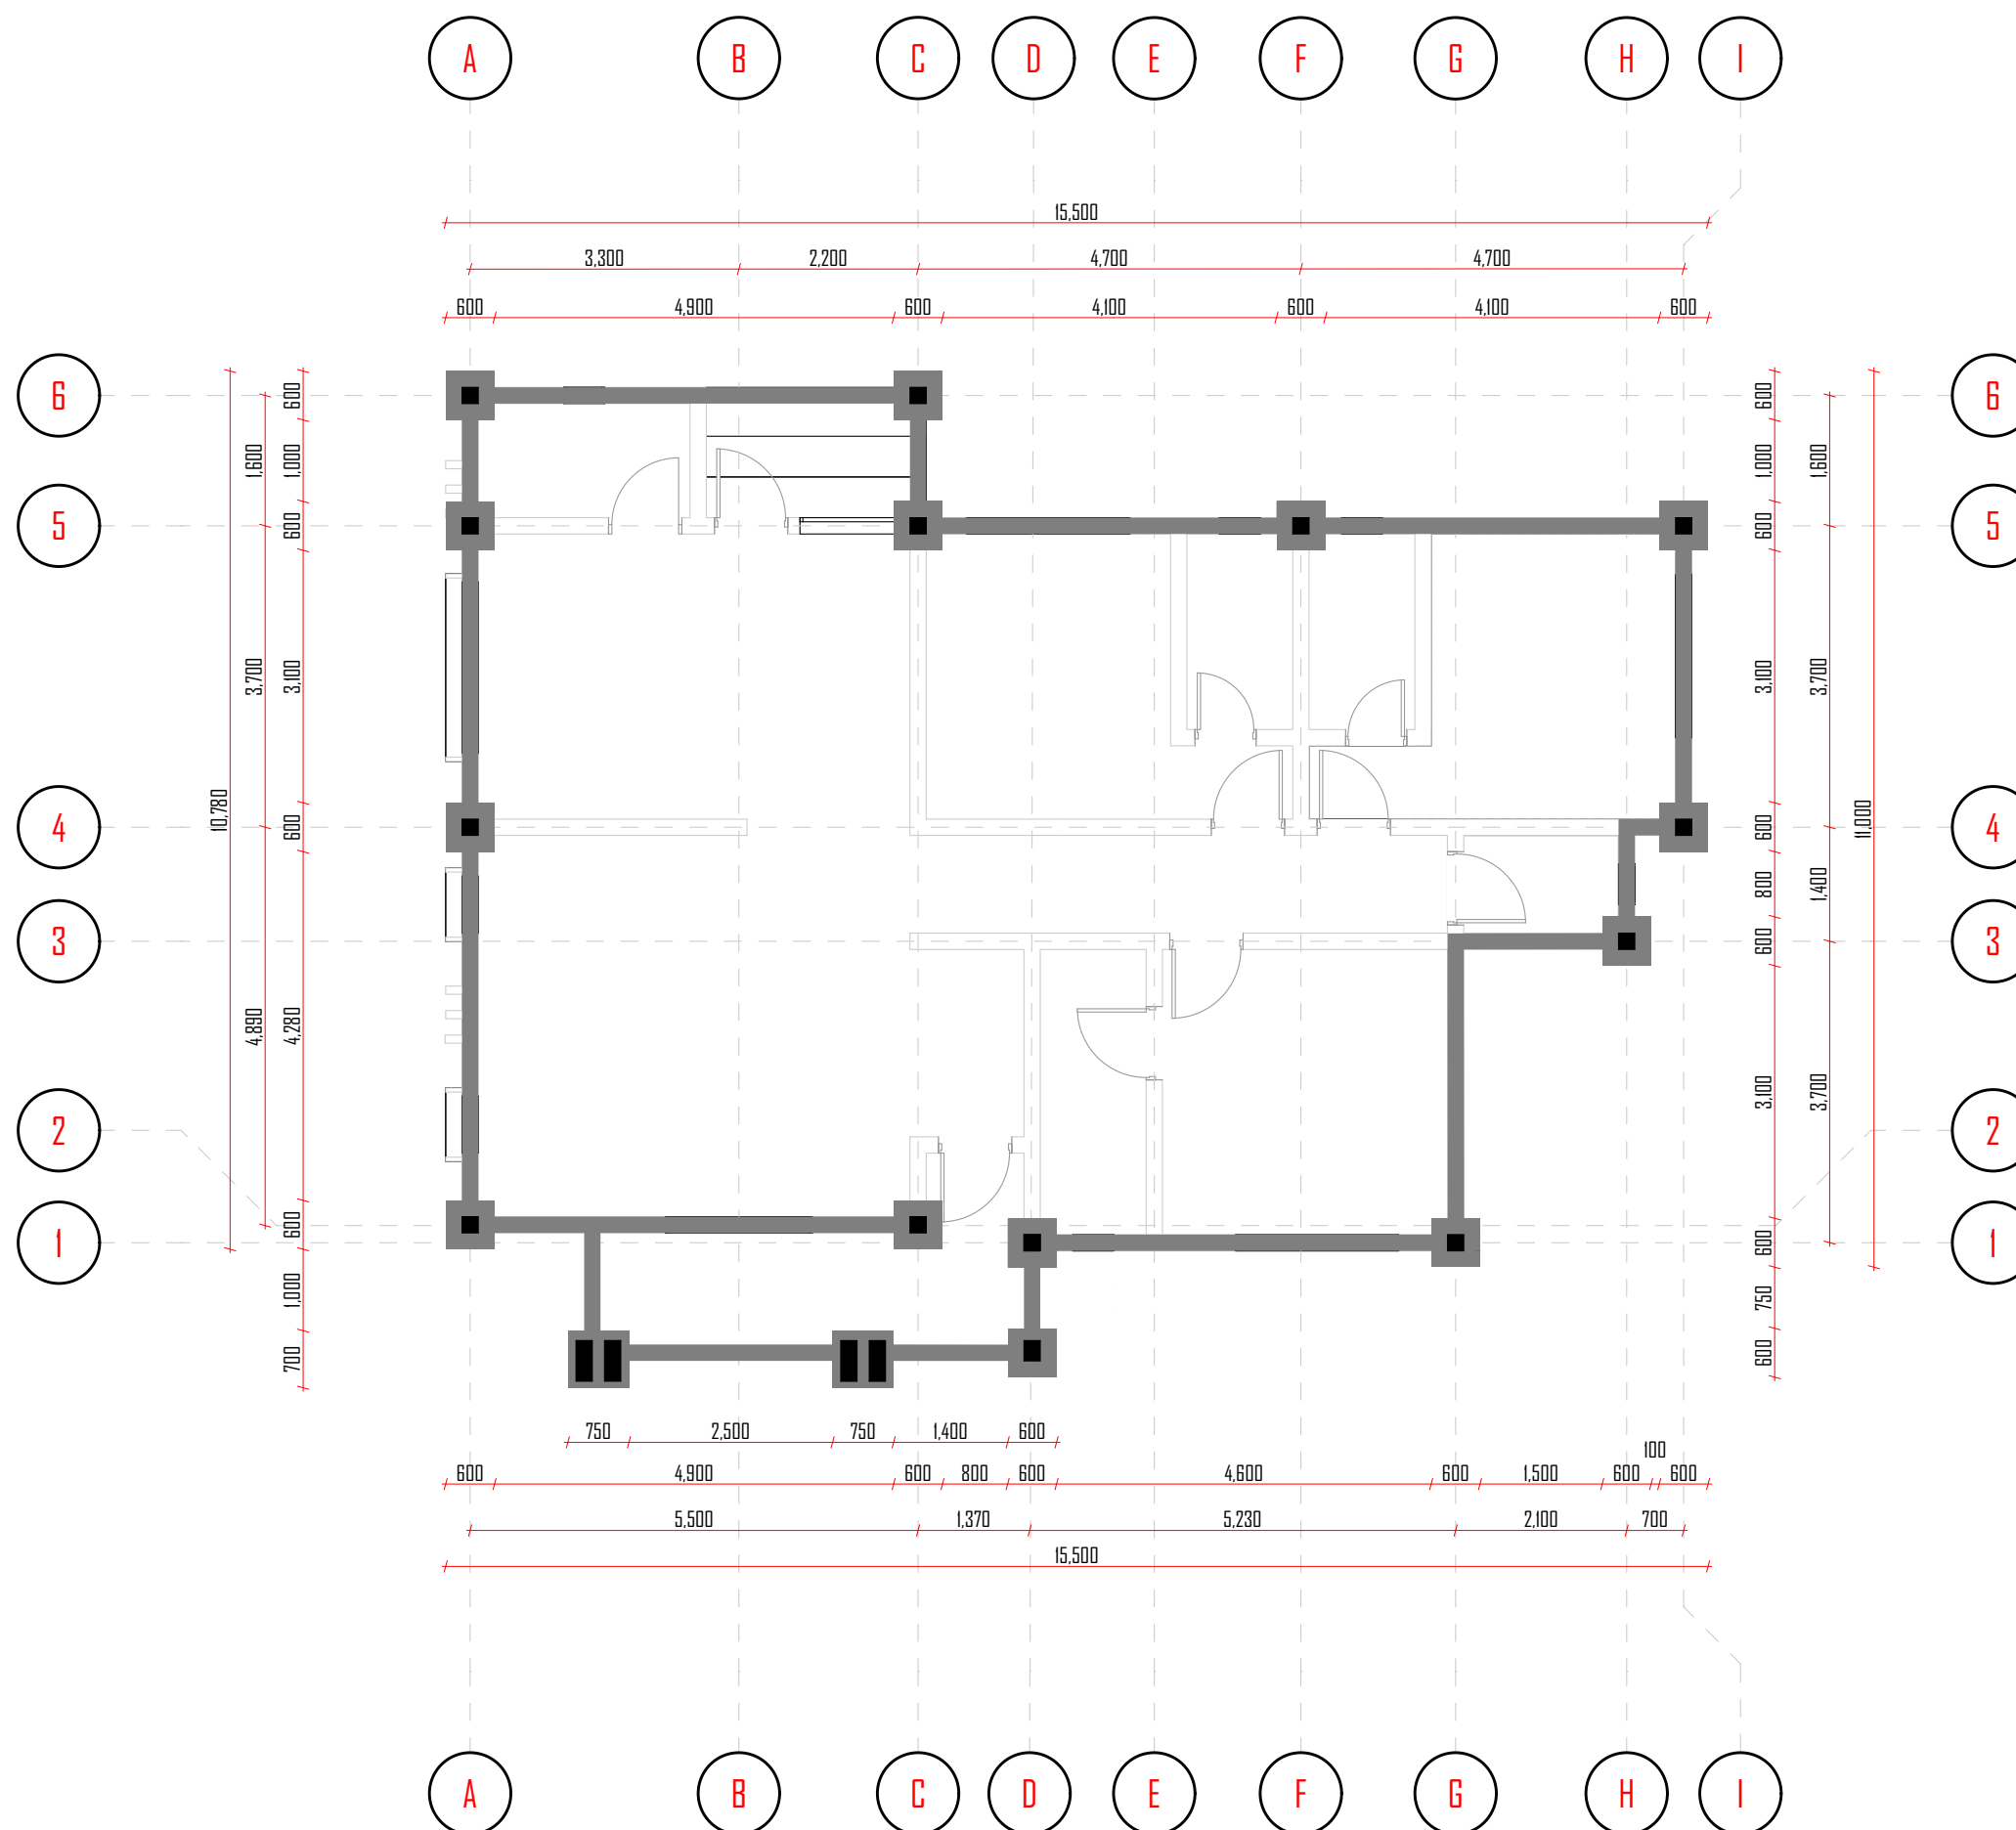

the KISERIAN HOUSE

NOTES


CLIENT

Ms. Linda Munyendo

Location: Kiserian, Kajiado

Plot Number: Kajiado/ OLCHORO onyore/ 34169

ORIENTATION

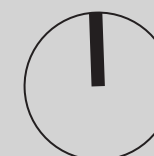


SCALE

1:100

Column Locations

A3.06

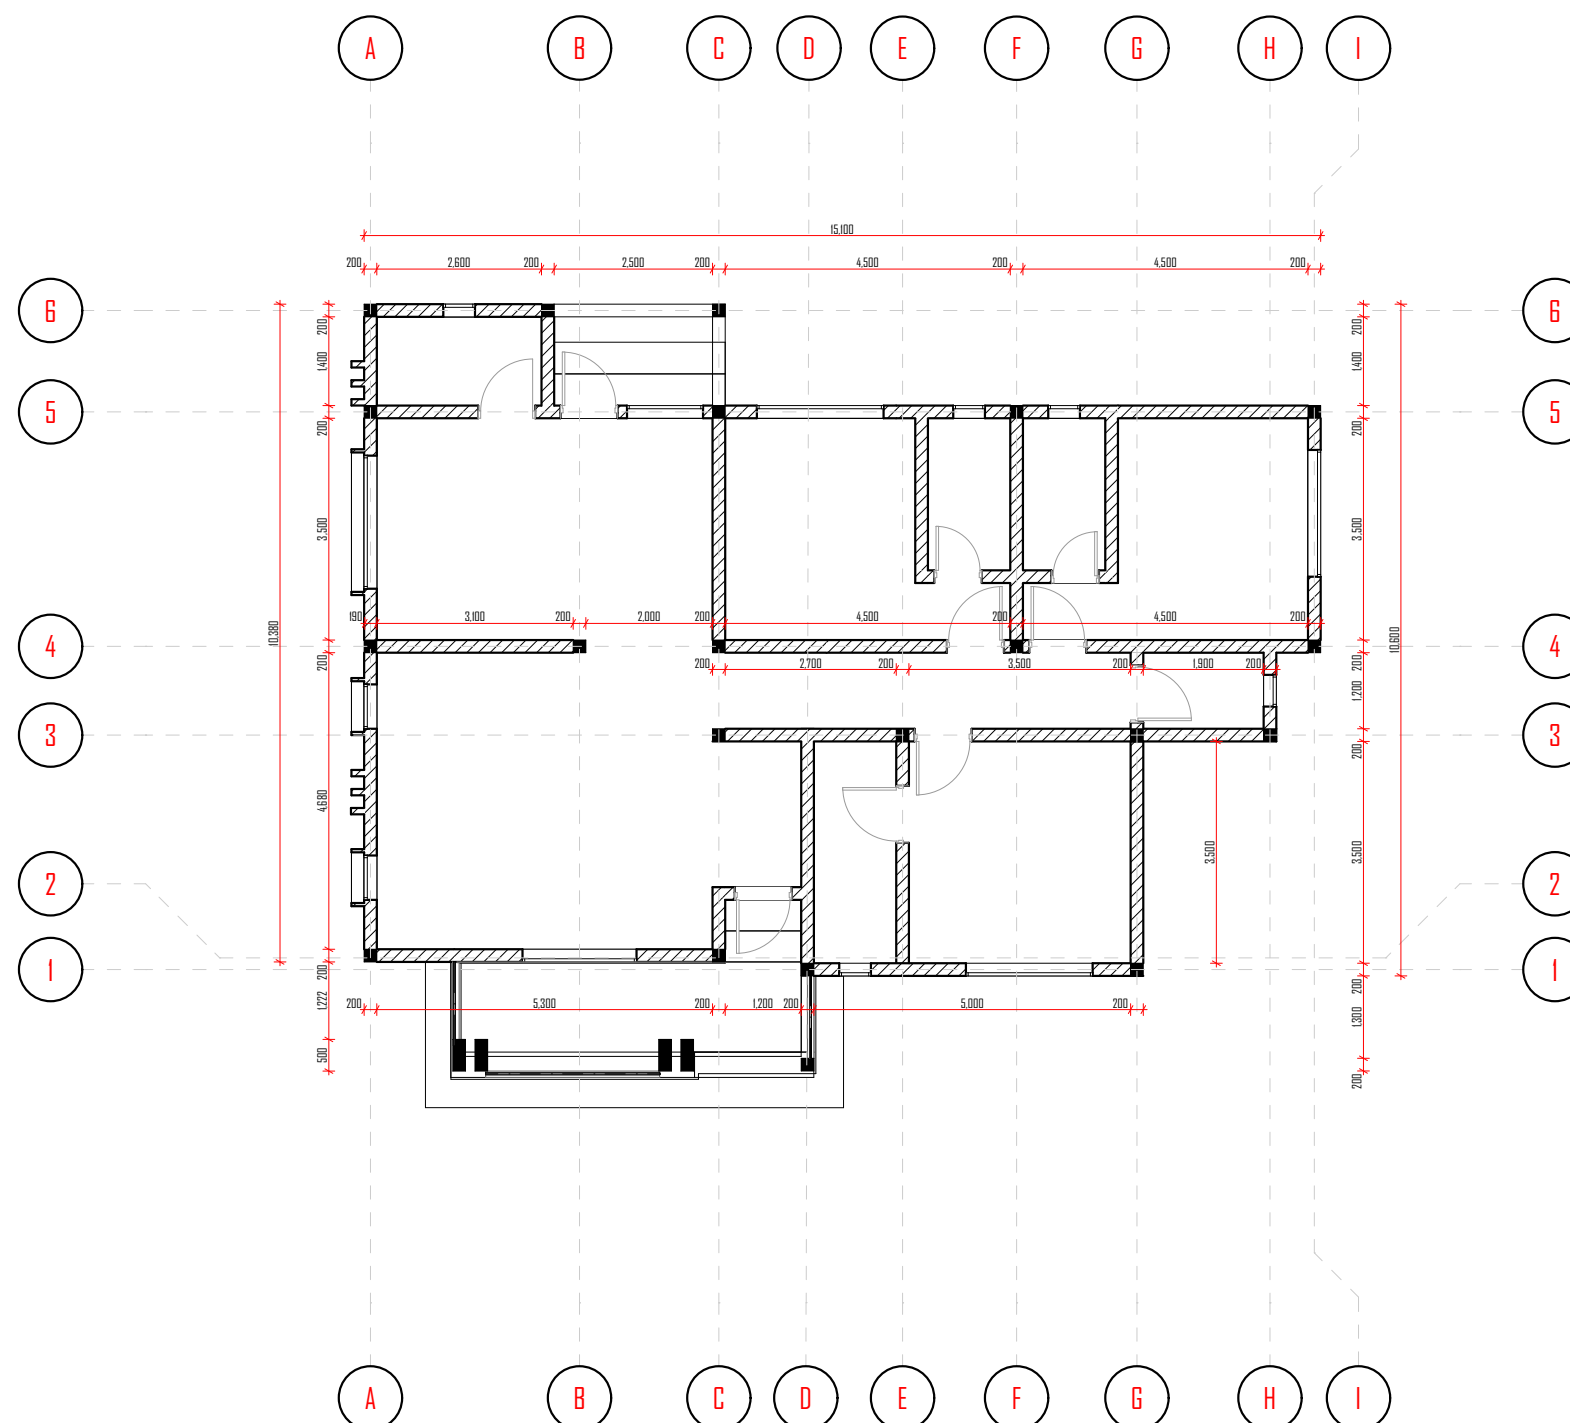

the KISERIAN HOUSE

NOTES

CLIENT

Ms. Linda Munyendo

Location: Kiserian, Kajiado

Plot Number: Kajiado/ OLCHORO onyore/ 34169

ORIENTATION




SCALE

1:100

Reflected Ceiling Plan
(Electrical)

A3.07

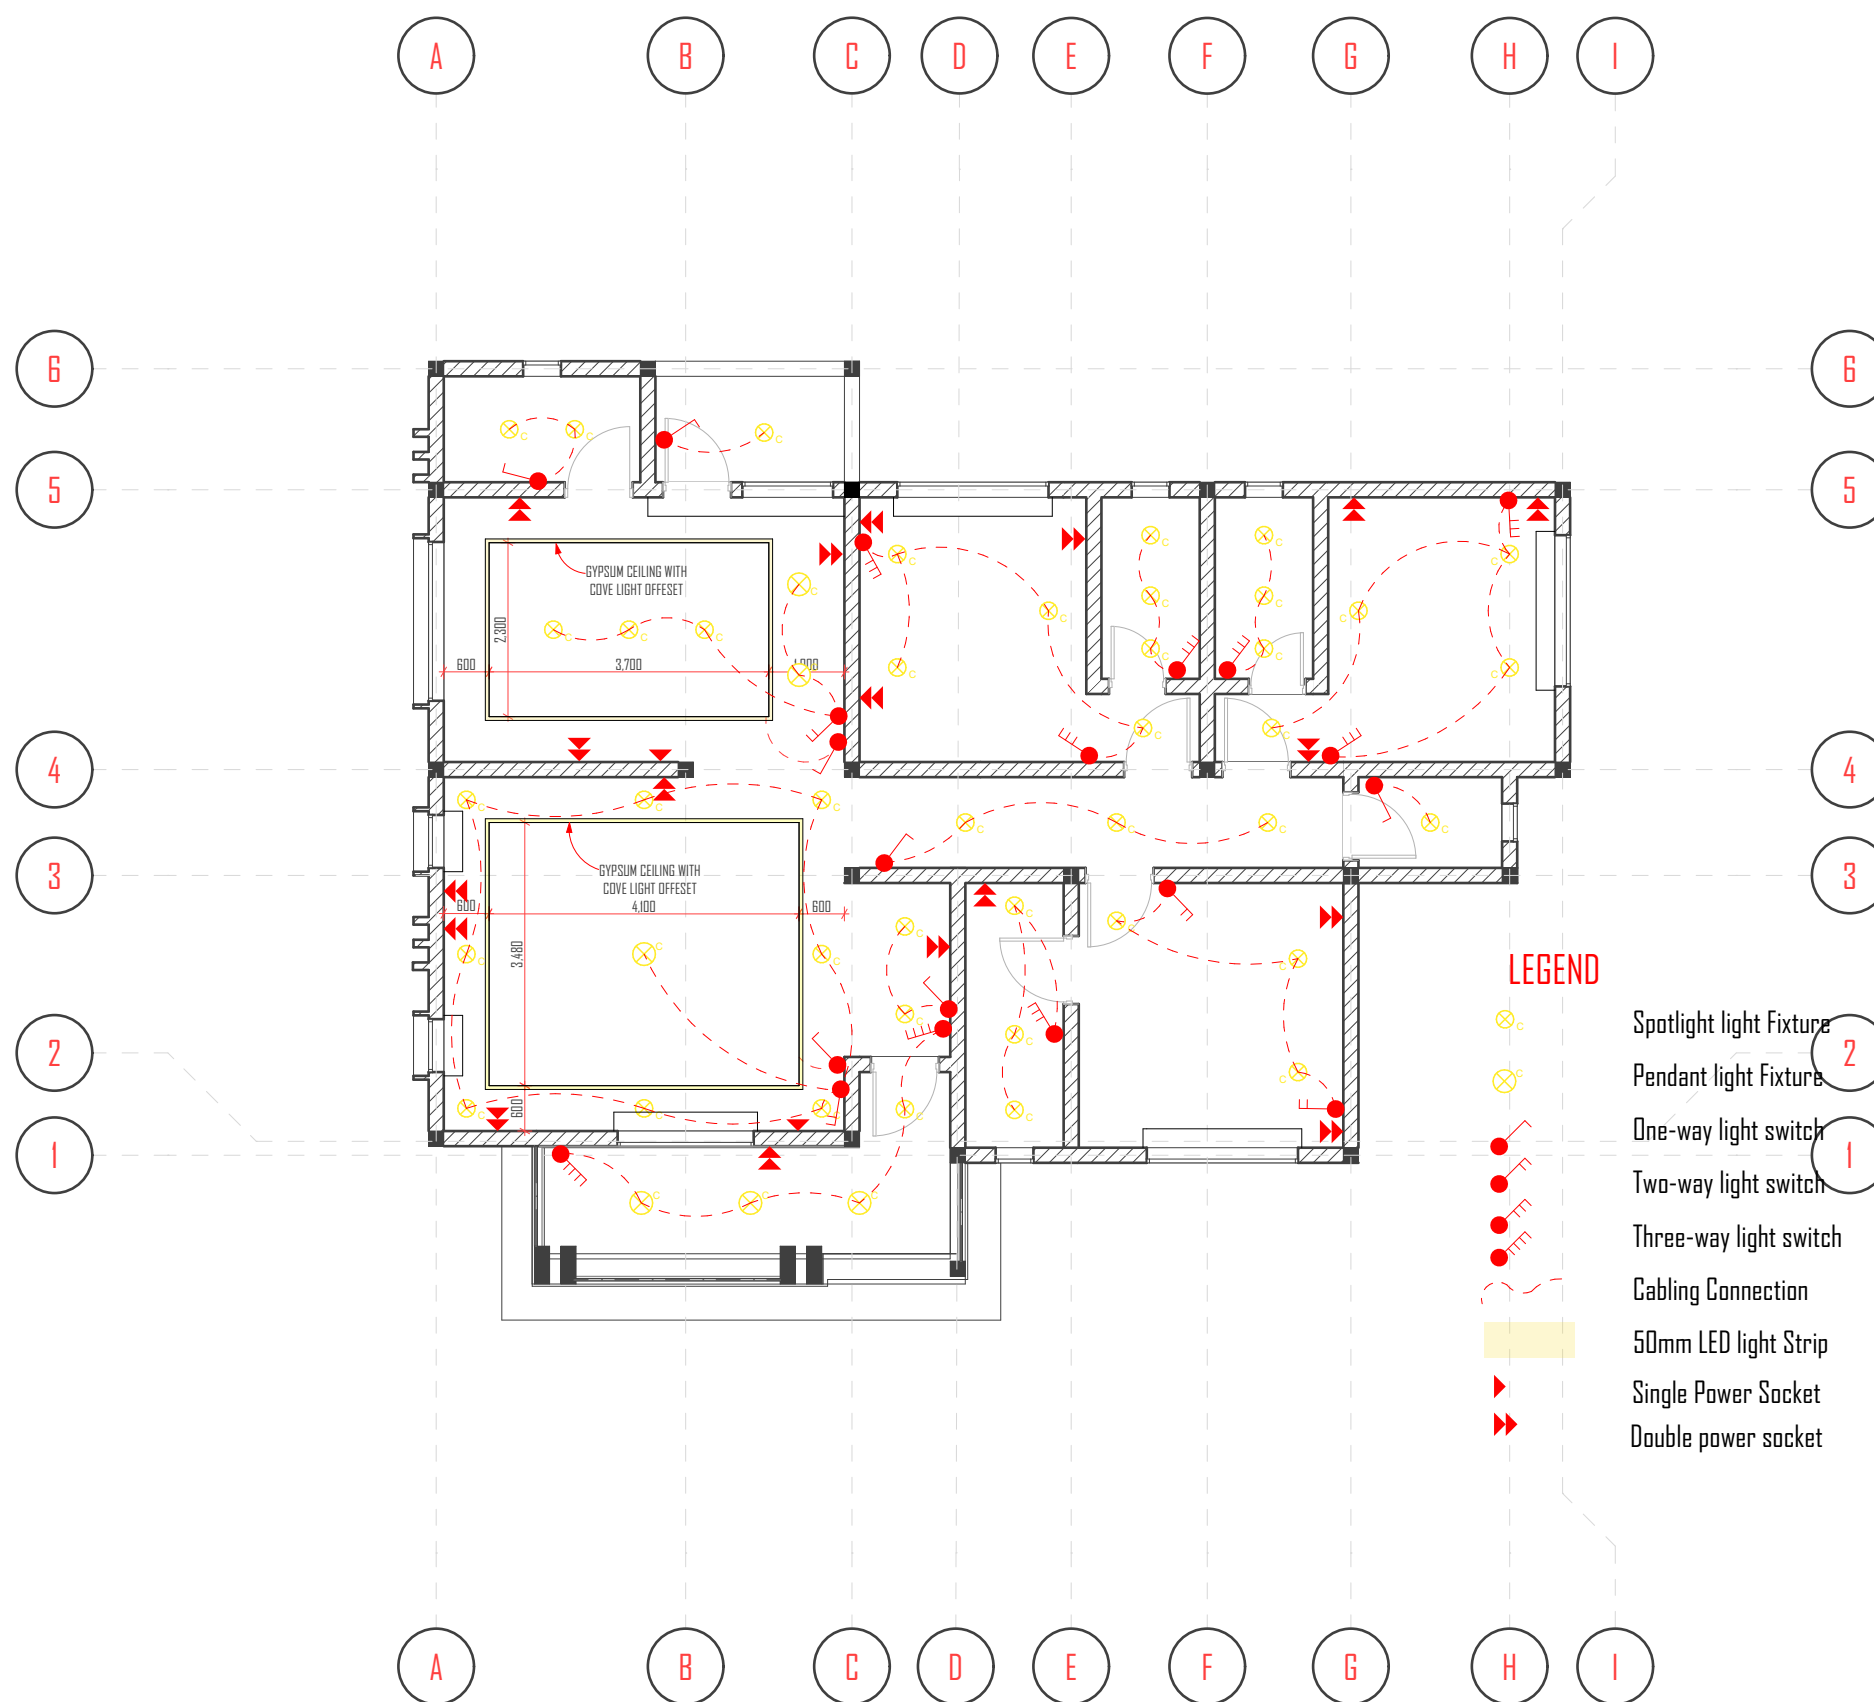

the **NIGERIAN HOUSE**

NOTES

CLIENT

Ms. Linda Munyendo

Location: Kiserian, Kajiado

Plot Number: Kajiado/ OLCHORO onyore/ 34169

ORIENTATION




SCALE 1:100

SCALE 1:100

Drainage Plan

A3.08

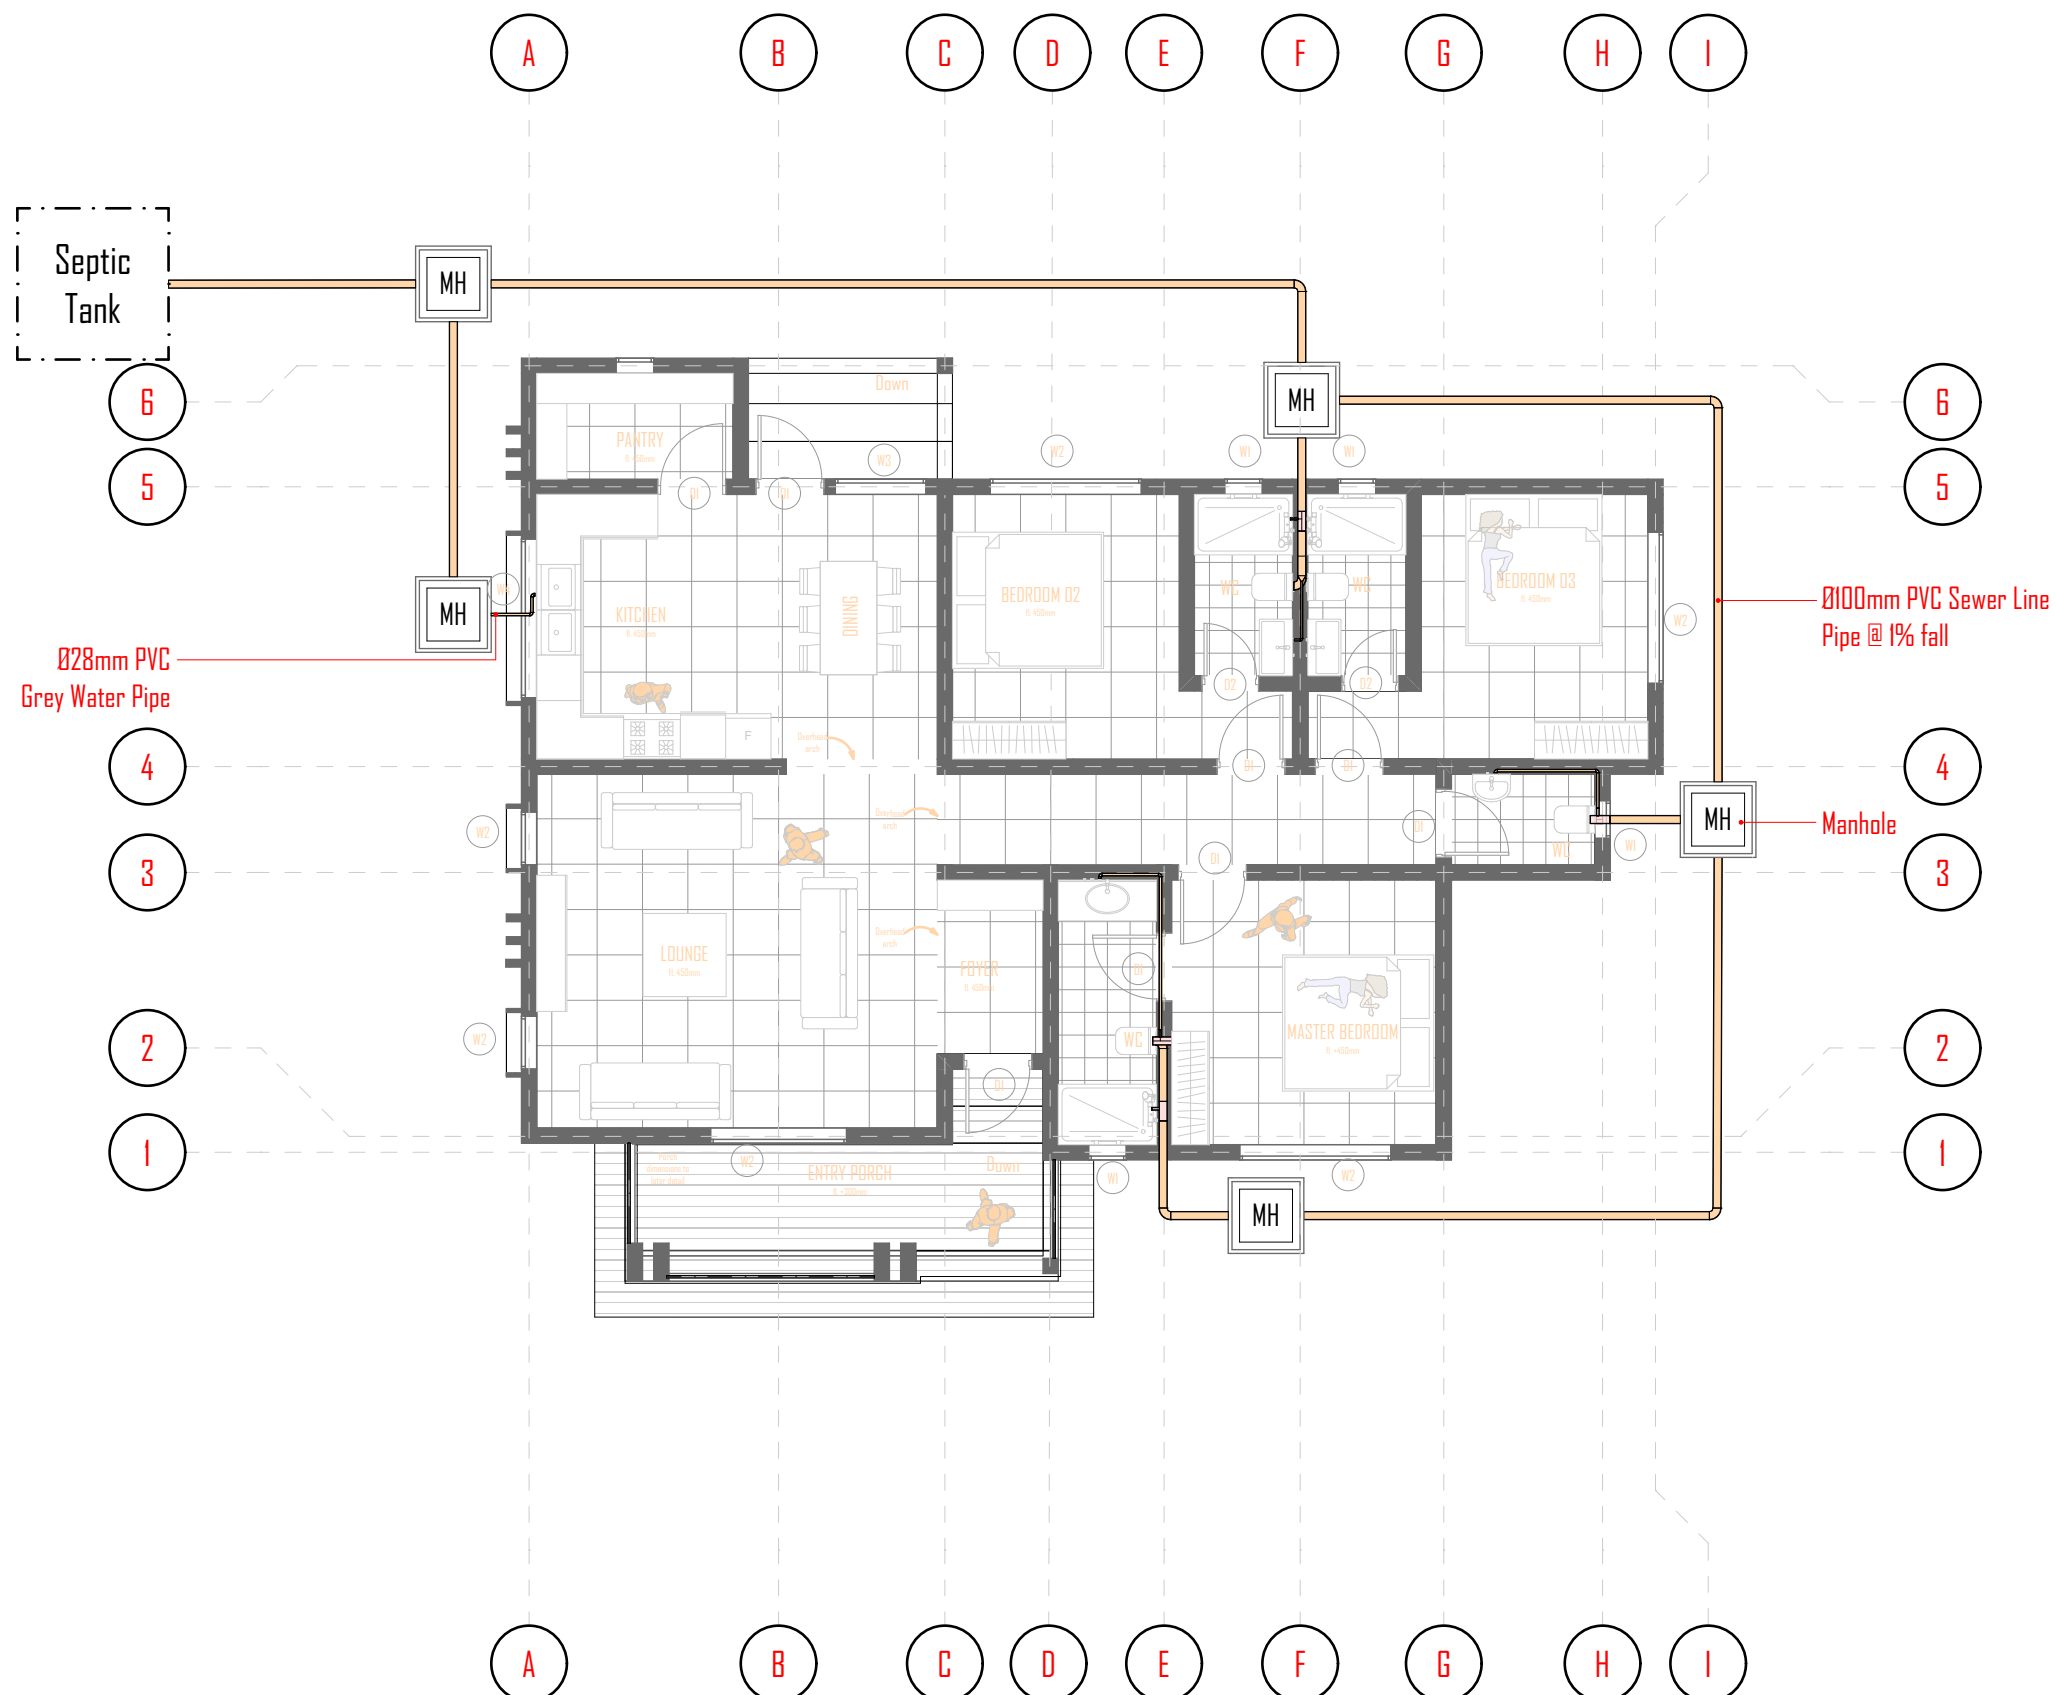

the **KISERIAN HOUSE**

NOTES

CLIENT

Ms. Linda Munyendo

Location: Kiserian, Kajiado

Plot Number: Kajiado/ OLCHORO onyore/ 34169

ORIENTATION




SCALE

1:100

Cold Water Supply

A3.09

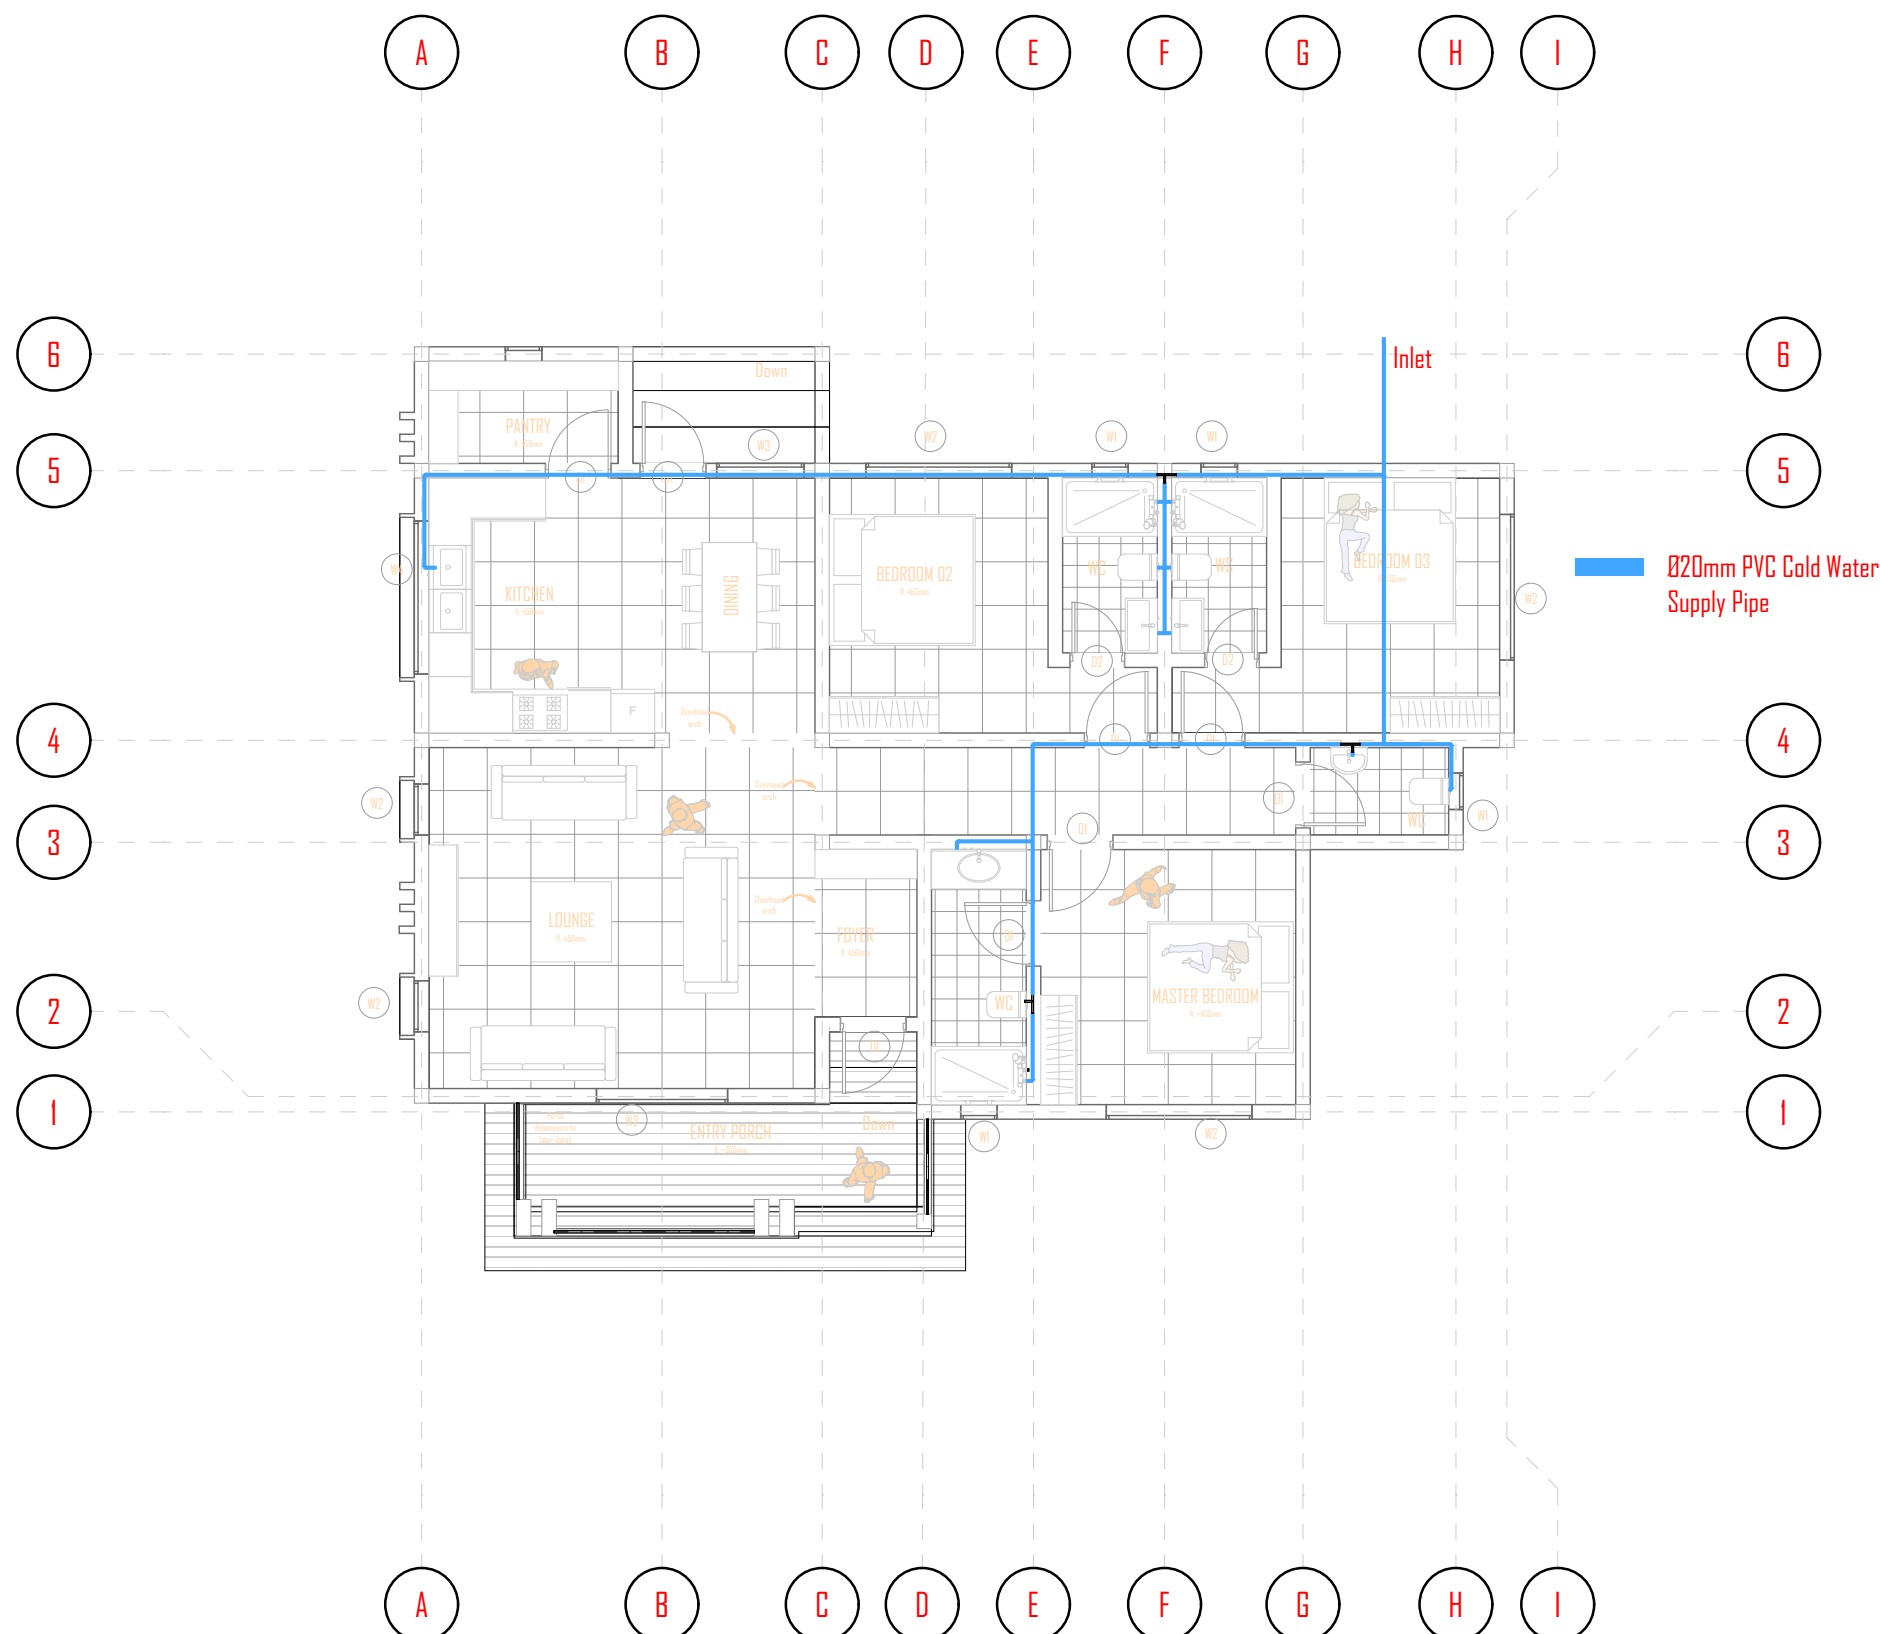

the **KISERIAN HOUSE**

NOTES

CLIENT
Ms. Linda Munyendo

Location: Kiserian, Kajiado

Plot Number: Kajiado/ OLCHORO onyore/ 34169

ORIENTATION



SCALE 1:200

Drainage Site Plan

A3.10



the **NIGERIAN HOUSE**

NOTES

CLIENT

Ms. Linda Munyendo

Location: Kiserian, Kajiado

Plot Number: Kajiado/ OLCHORO onyore/ 34169

ORIENTATION




SCALE 1:100

1:100

Roof Plan

A3.11

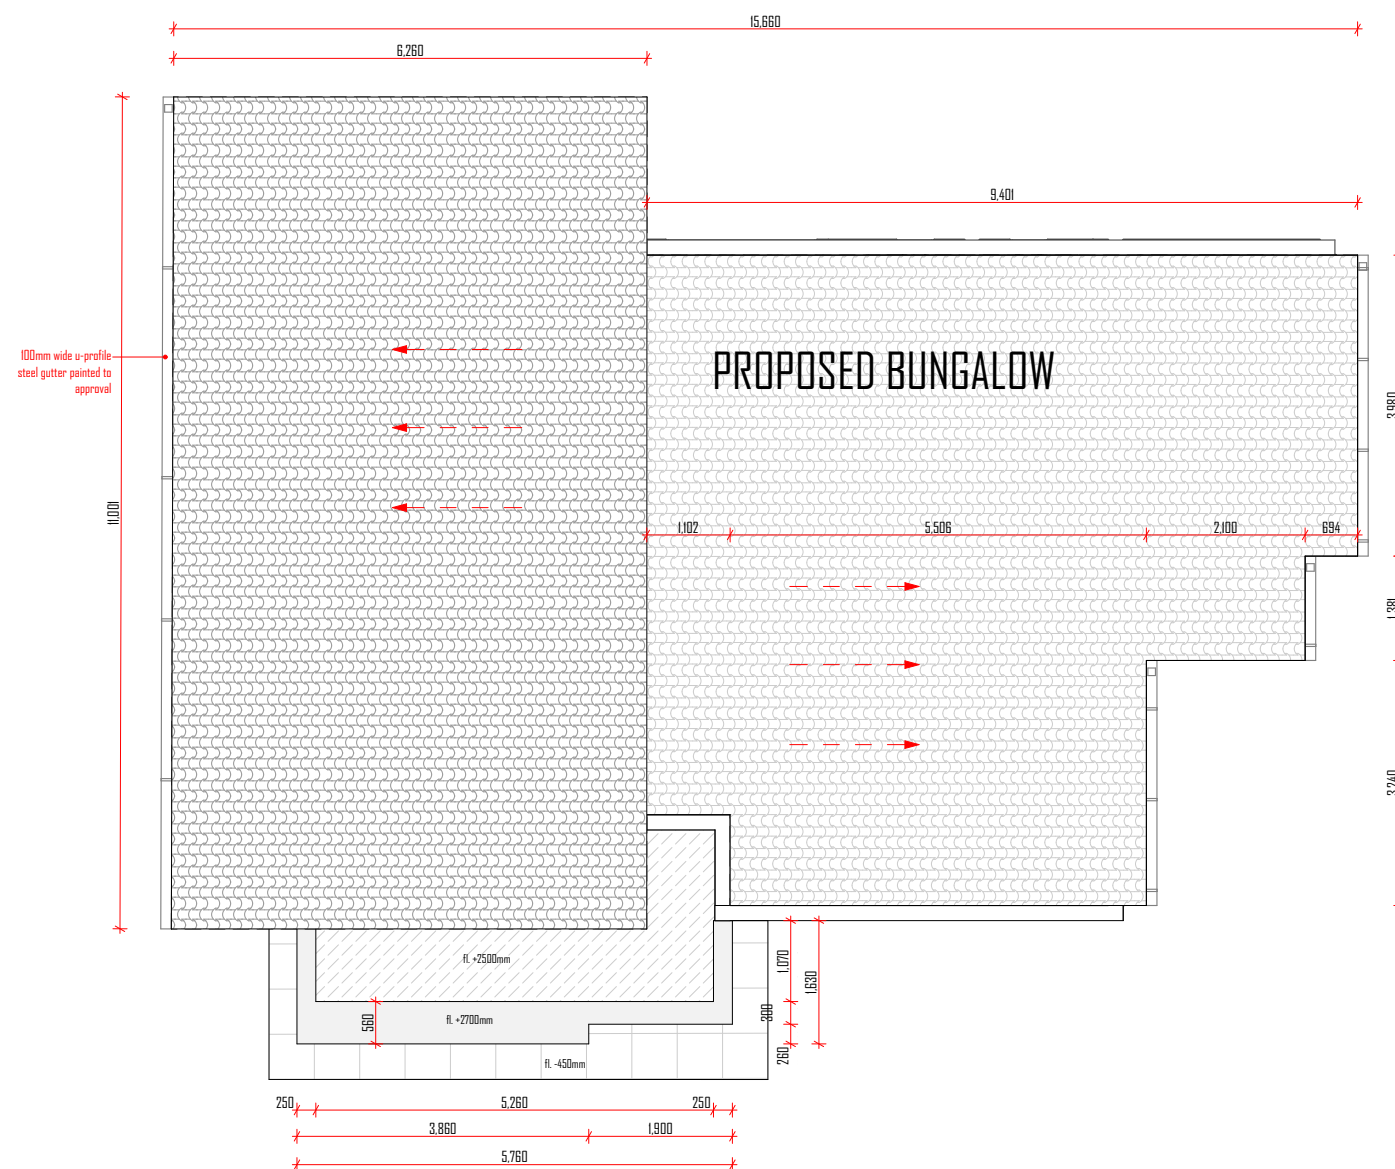

the KISERIAN HOUSE

NOTES

CLIENT

Ms. Linda Munyendo

Location: Kiserian, Kajiado

Plot Number: Kajiado/ OLCHORO onyore/ 34169

ORIENTATION



SCALE

1:100

Elevation 01

A3.12



the **KISERIAN HOUSE**

NOTES

CLIENT

Ms. Linda Munyendo

Location: Kiserian, Kajiado

Plot Number: Kajiado/ OLCHORO onyore/ 34169

ORIENTATION




SCALE

1:100

Elevation 02

A3.13

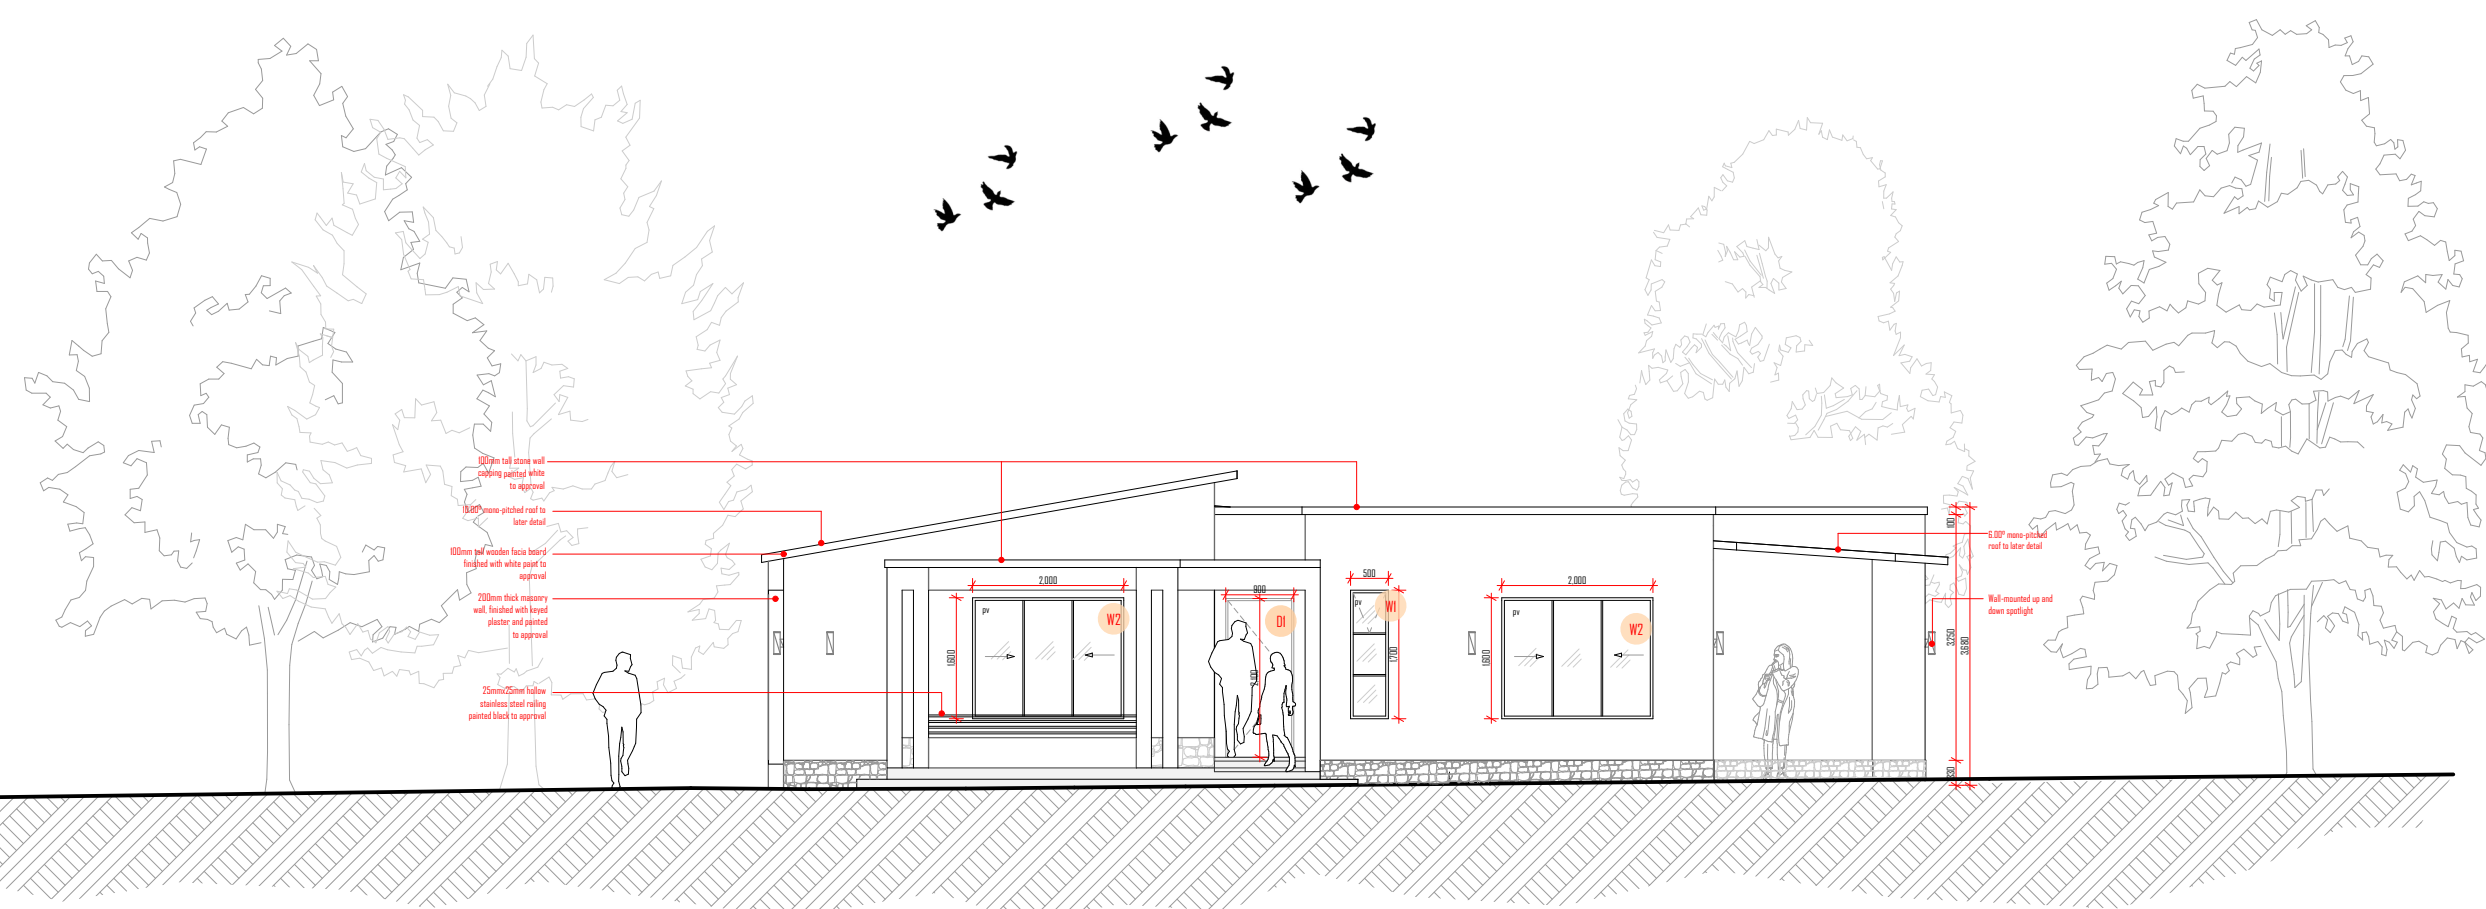

the **KISERIAN HOUSE**

NOTES


CLIENT

Ms. Linda Munyendo

Location: Kiserian, Kajiado

Plot Number: Kajiado/ OLCHORO onyore/ 34169

ORIENTATION

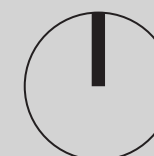


SCALE

1:100

Elevation 03

A3.14

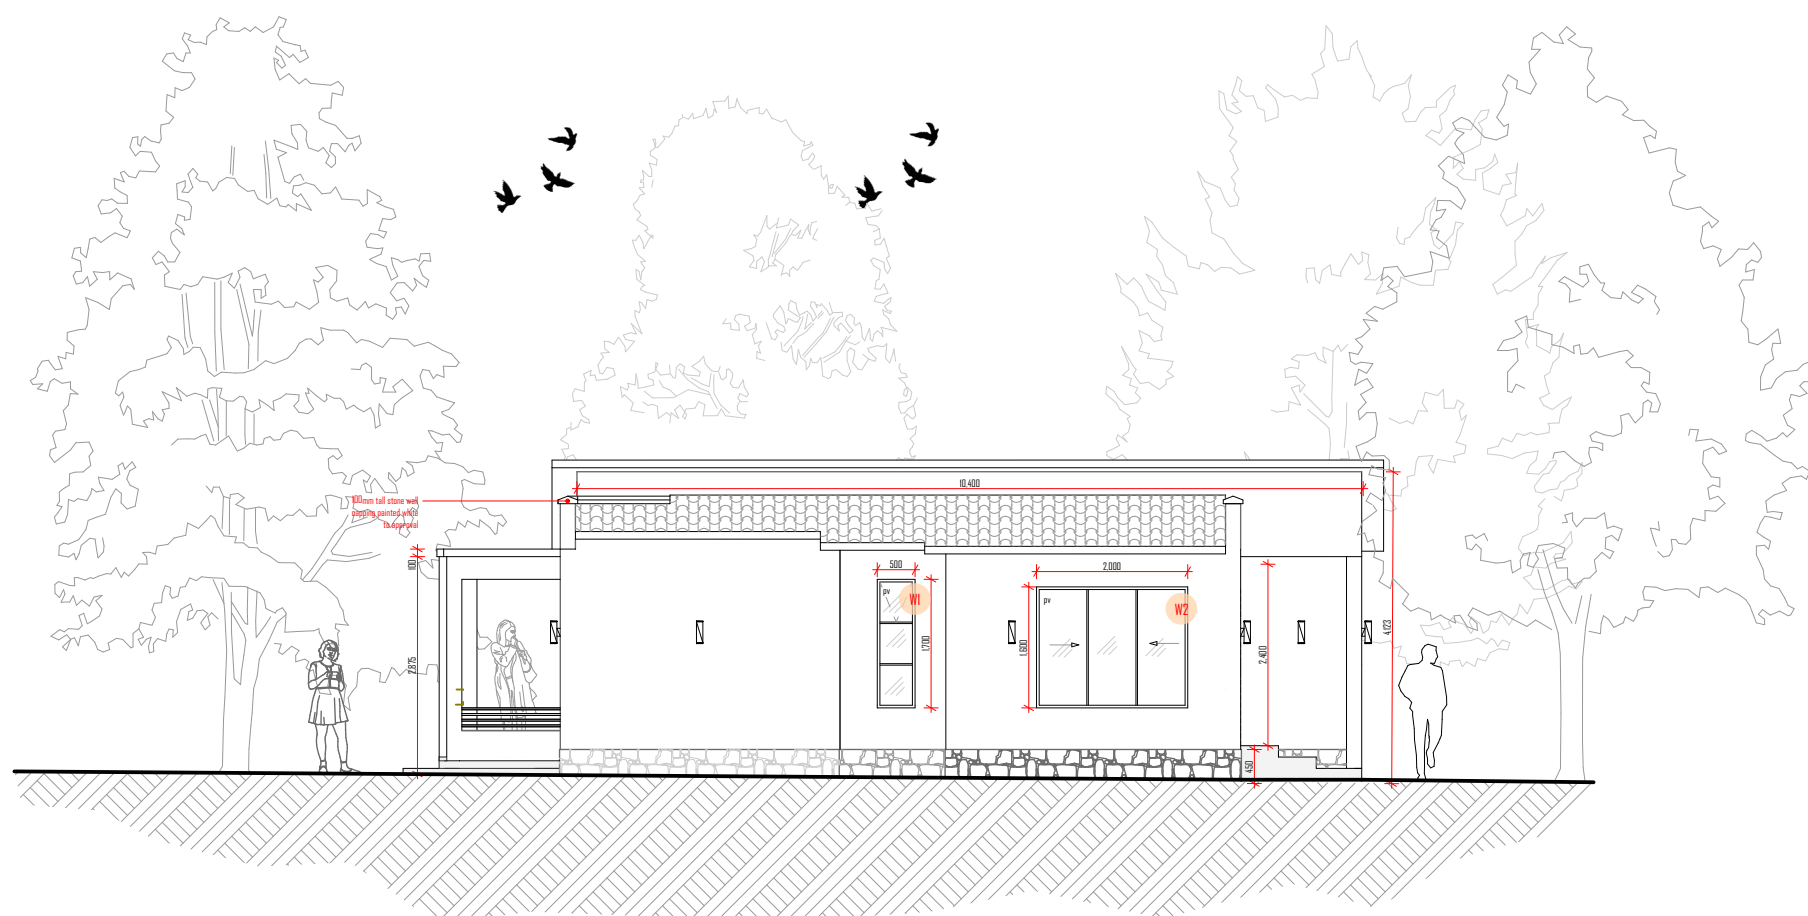

the **KISERIAN HOUSE**

NOTES

CLIENT

Ms. Linda Munyendo

Location: Kiserian, Kajiado

Plot Number: Kajiado/ OLCHORO onyore/ 34169

ORIENTATION




SCALE

1:100

Elevation 04

A3.15

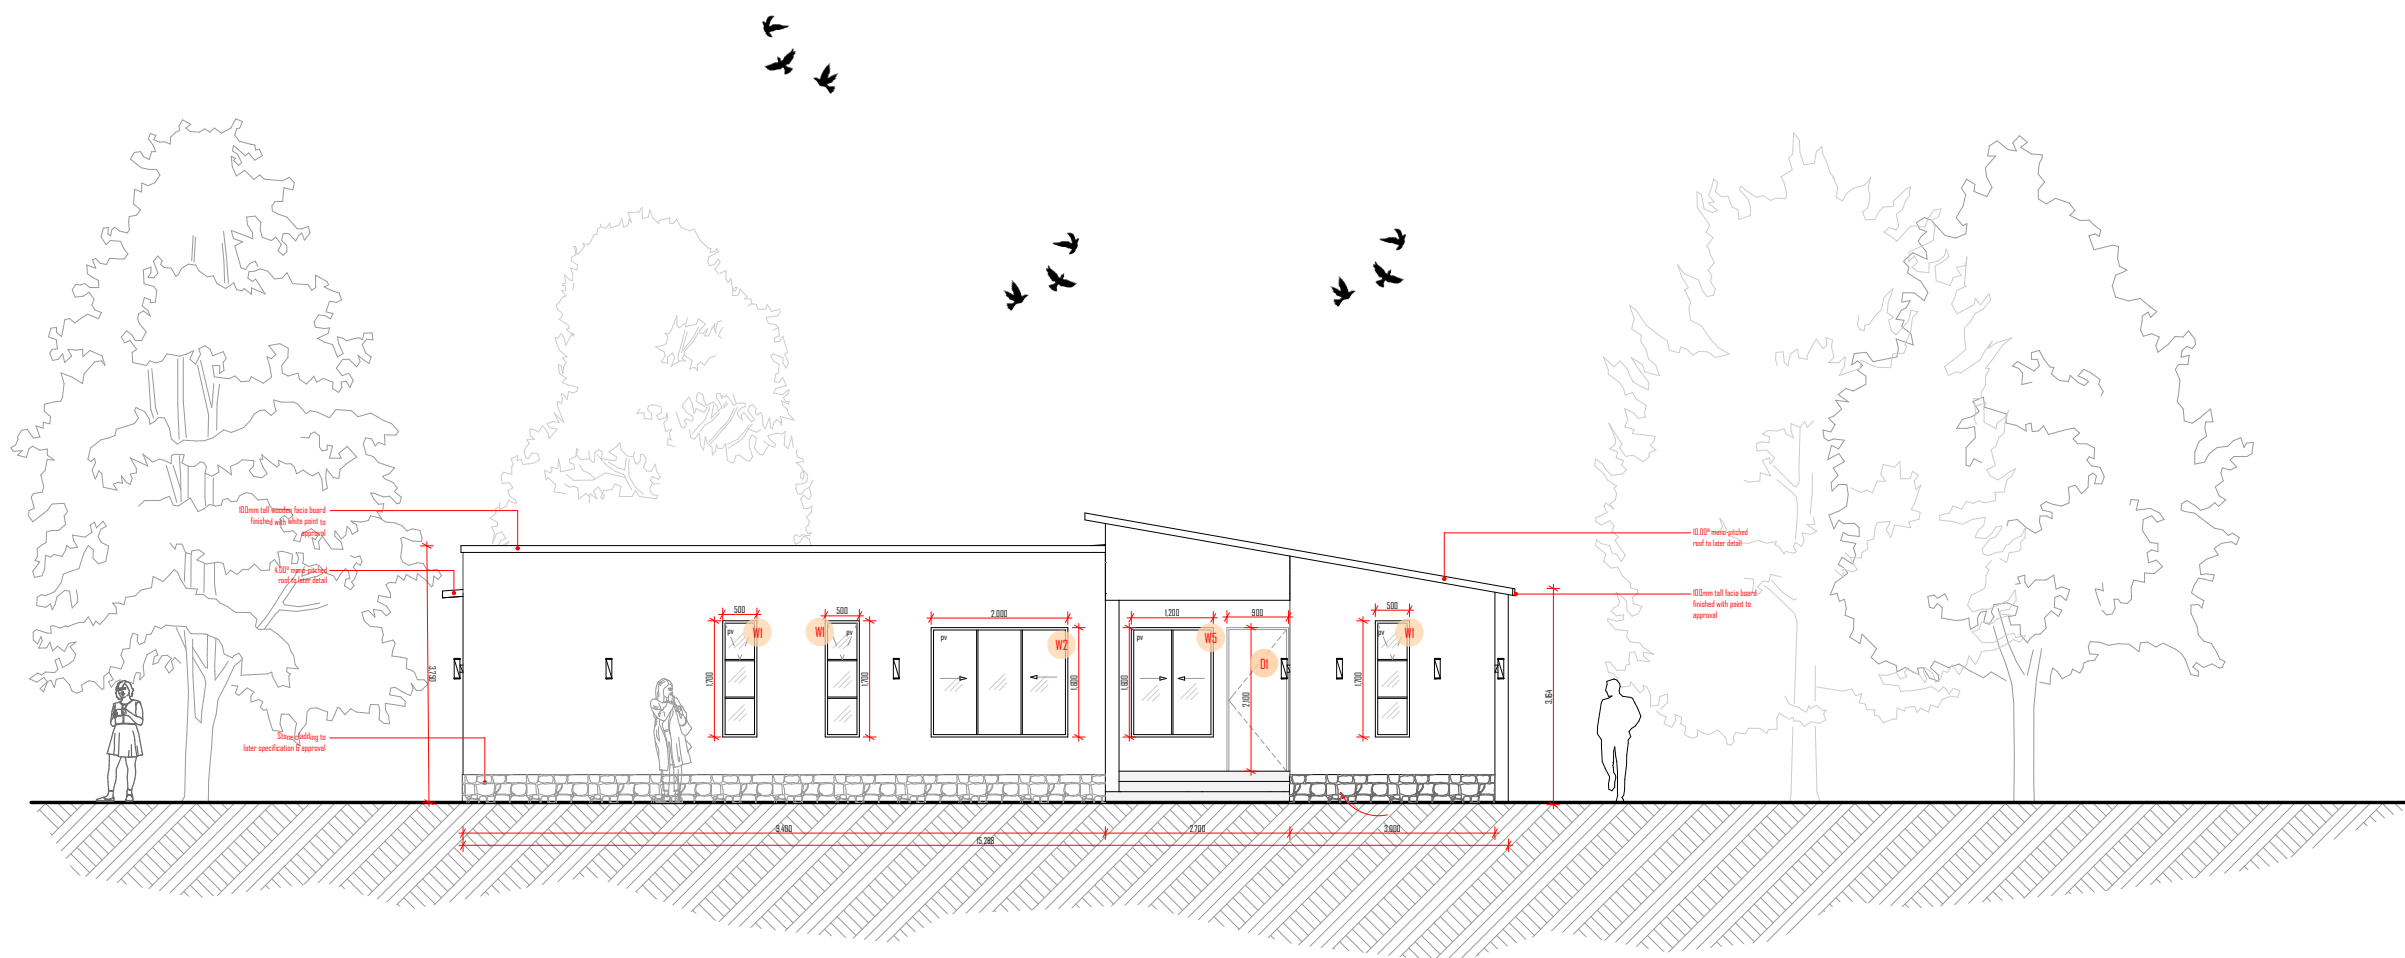

the KISERIAN HOUSE

NOTES


CLIENT

Ms. Linda Munyendo

Location: Kiserian, Kajiado

Plot Number: Kajiado/ OLCHORO onyore/ 34169

ORIENTATION

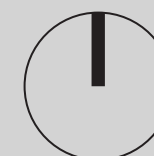


SCALE

1:100

Section 01

A3.16

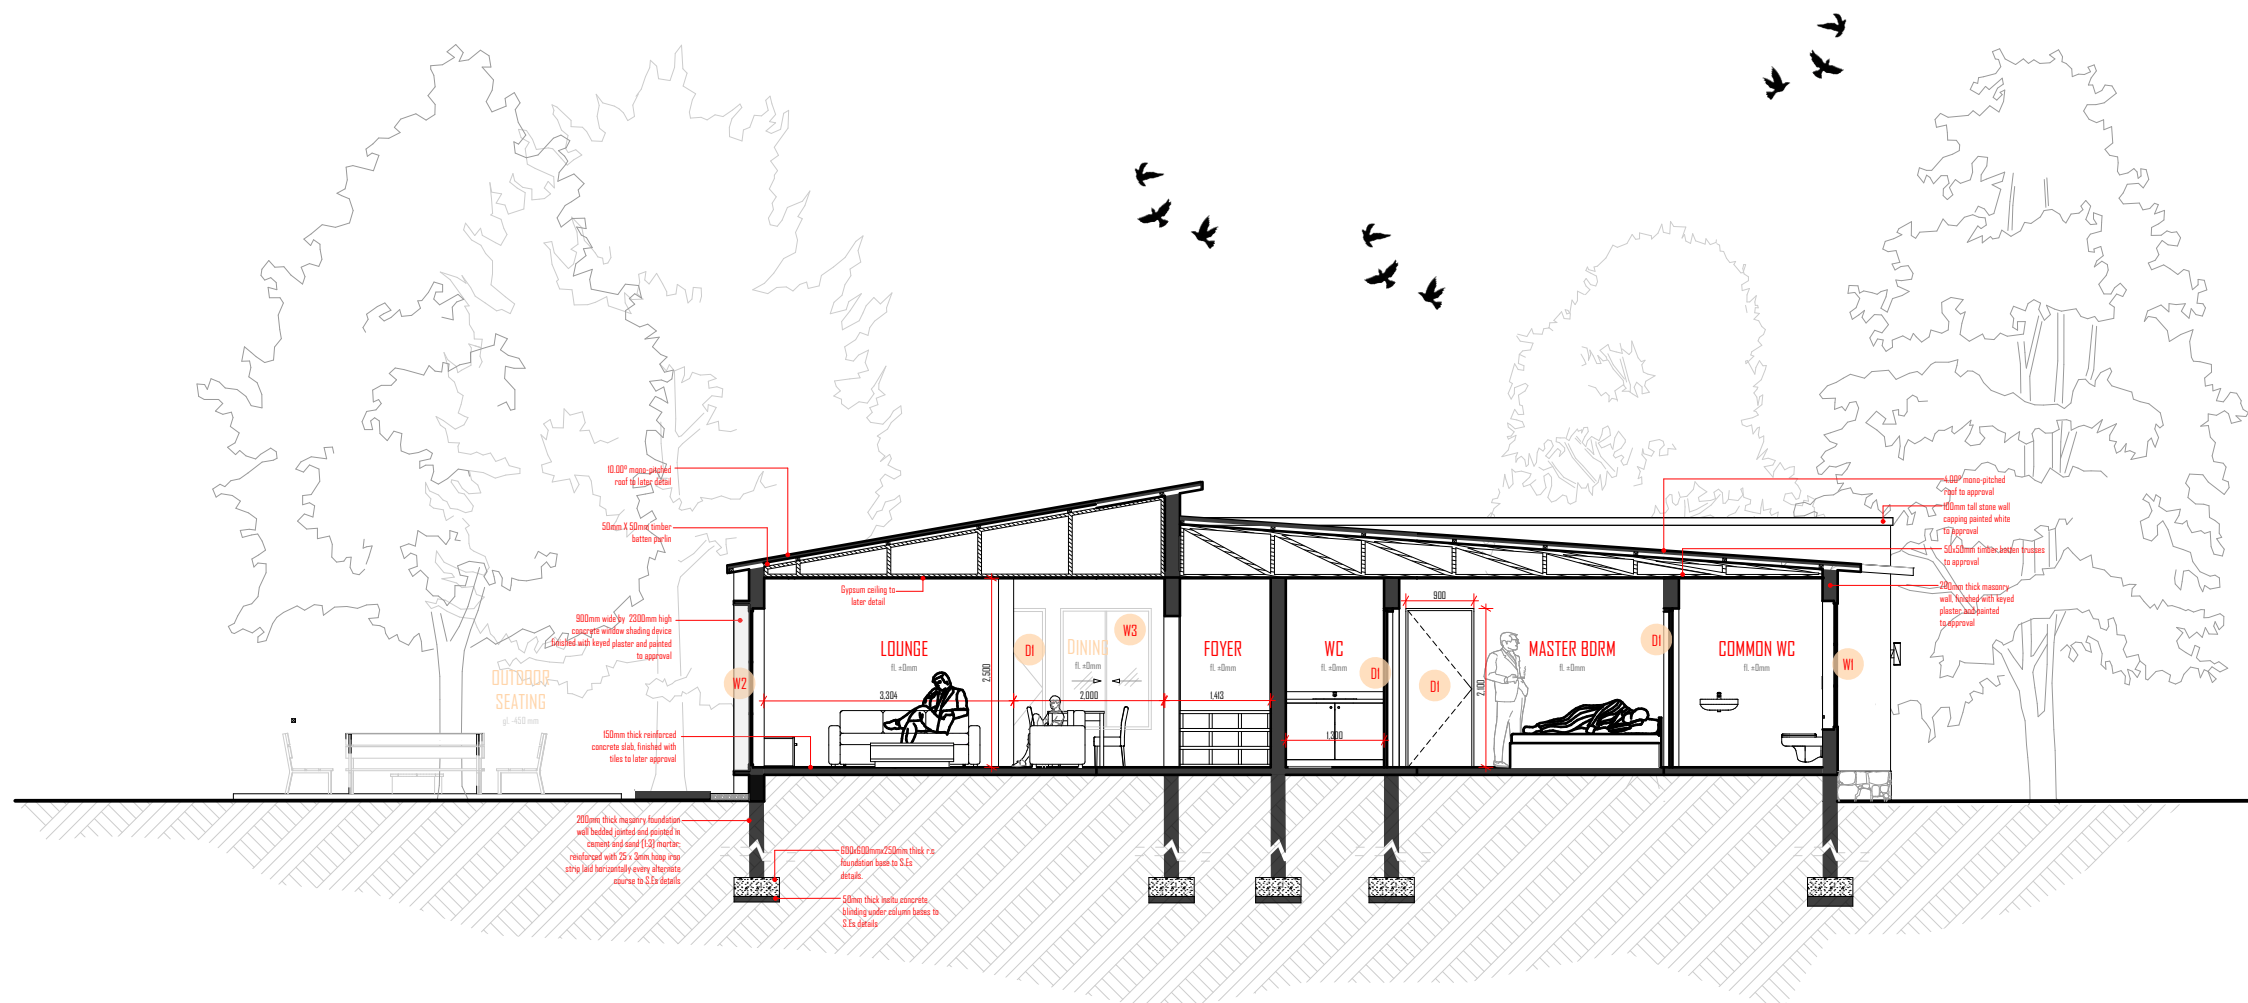

the **KISERIAN HOUSE**

NOTES

CLIENT

Ms. Linda Munyendo

Location: Kiserian, Kajiado

Plot Number: Kajiado/ OLCHORO onyore/ 34169

ORIENTATION




SCALE


1:50

Porch Details

A3.17

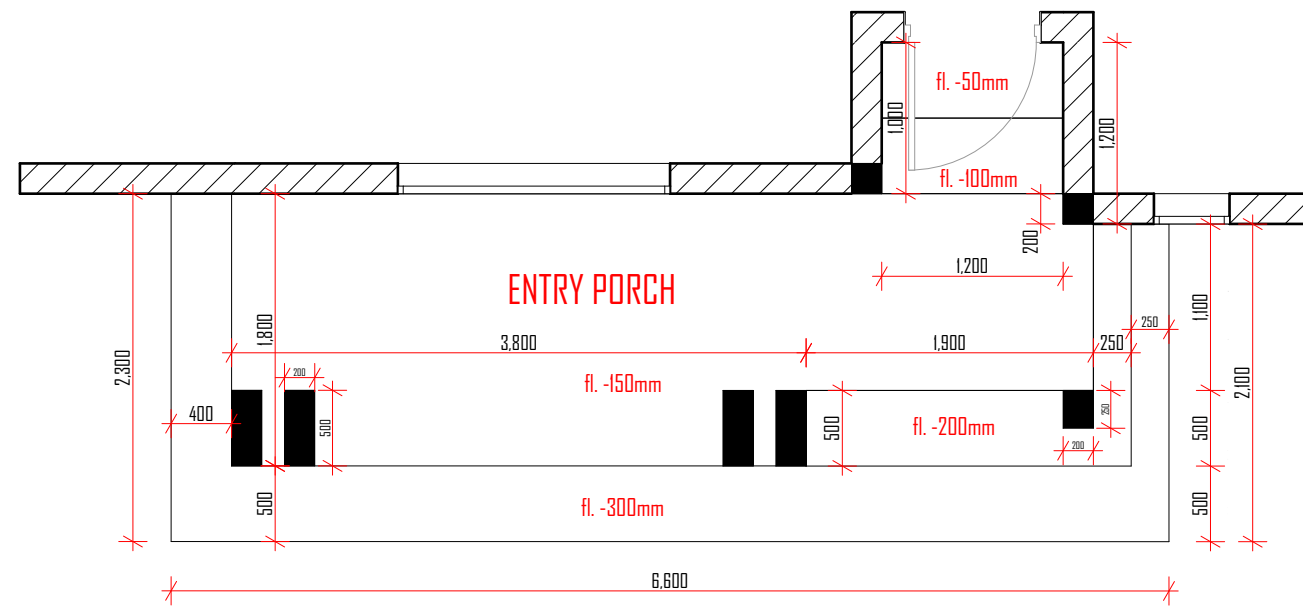

Floor Plan

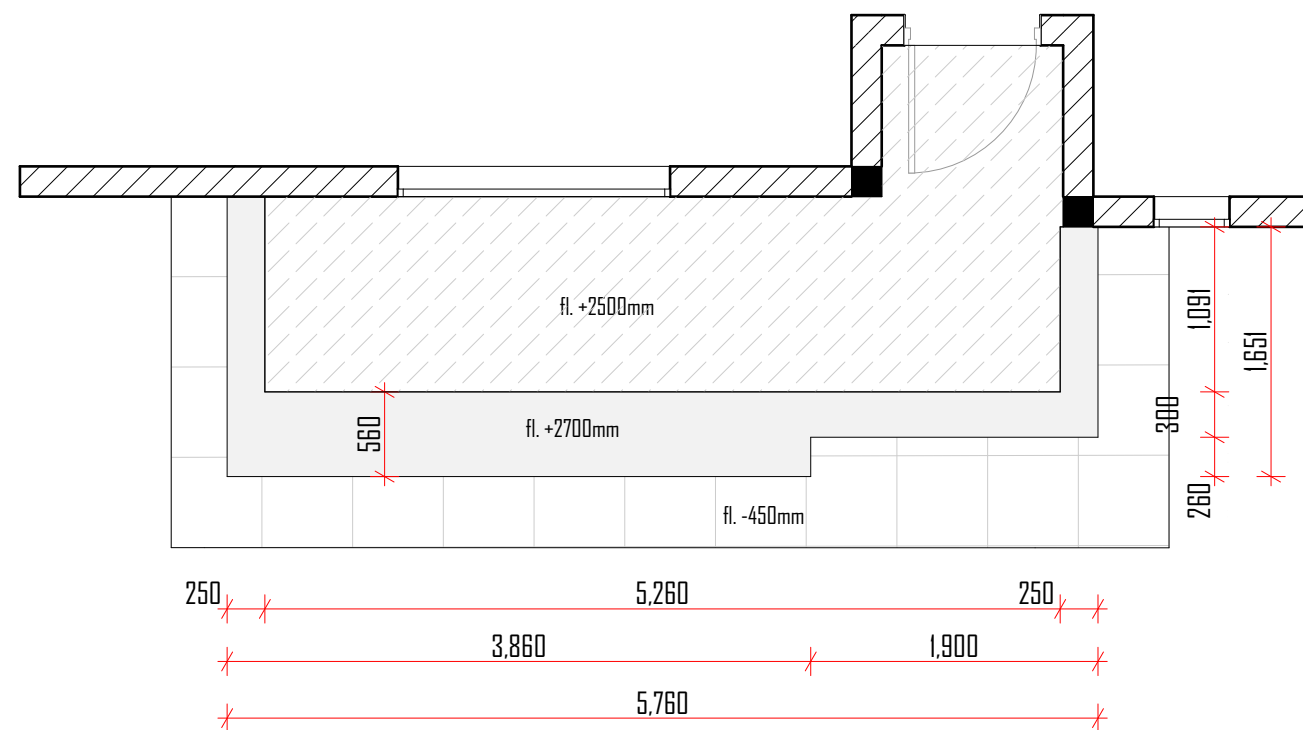

Roof Plan

the **KISERIAN HOUSE**

NOTES

CLIENT

Ms. Linda Munyendo

Location: Kiserian, Kajiado

Plot Number: Kajiado/ OLCHORO onyore/ 34169

ORIENTATION




SCALE

1:50

Septic Tank Details

A3.18

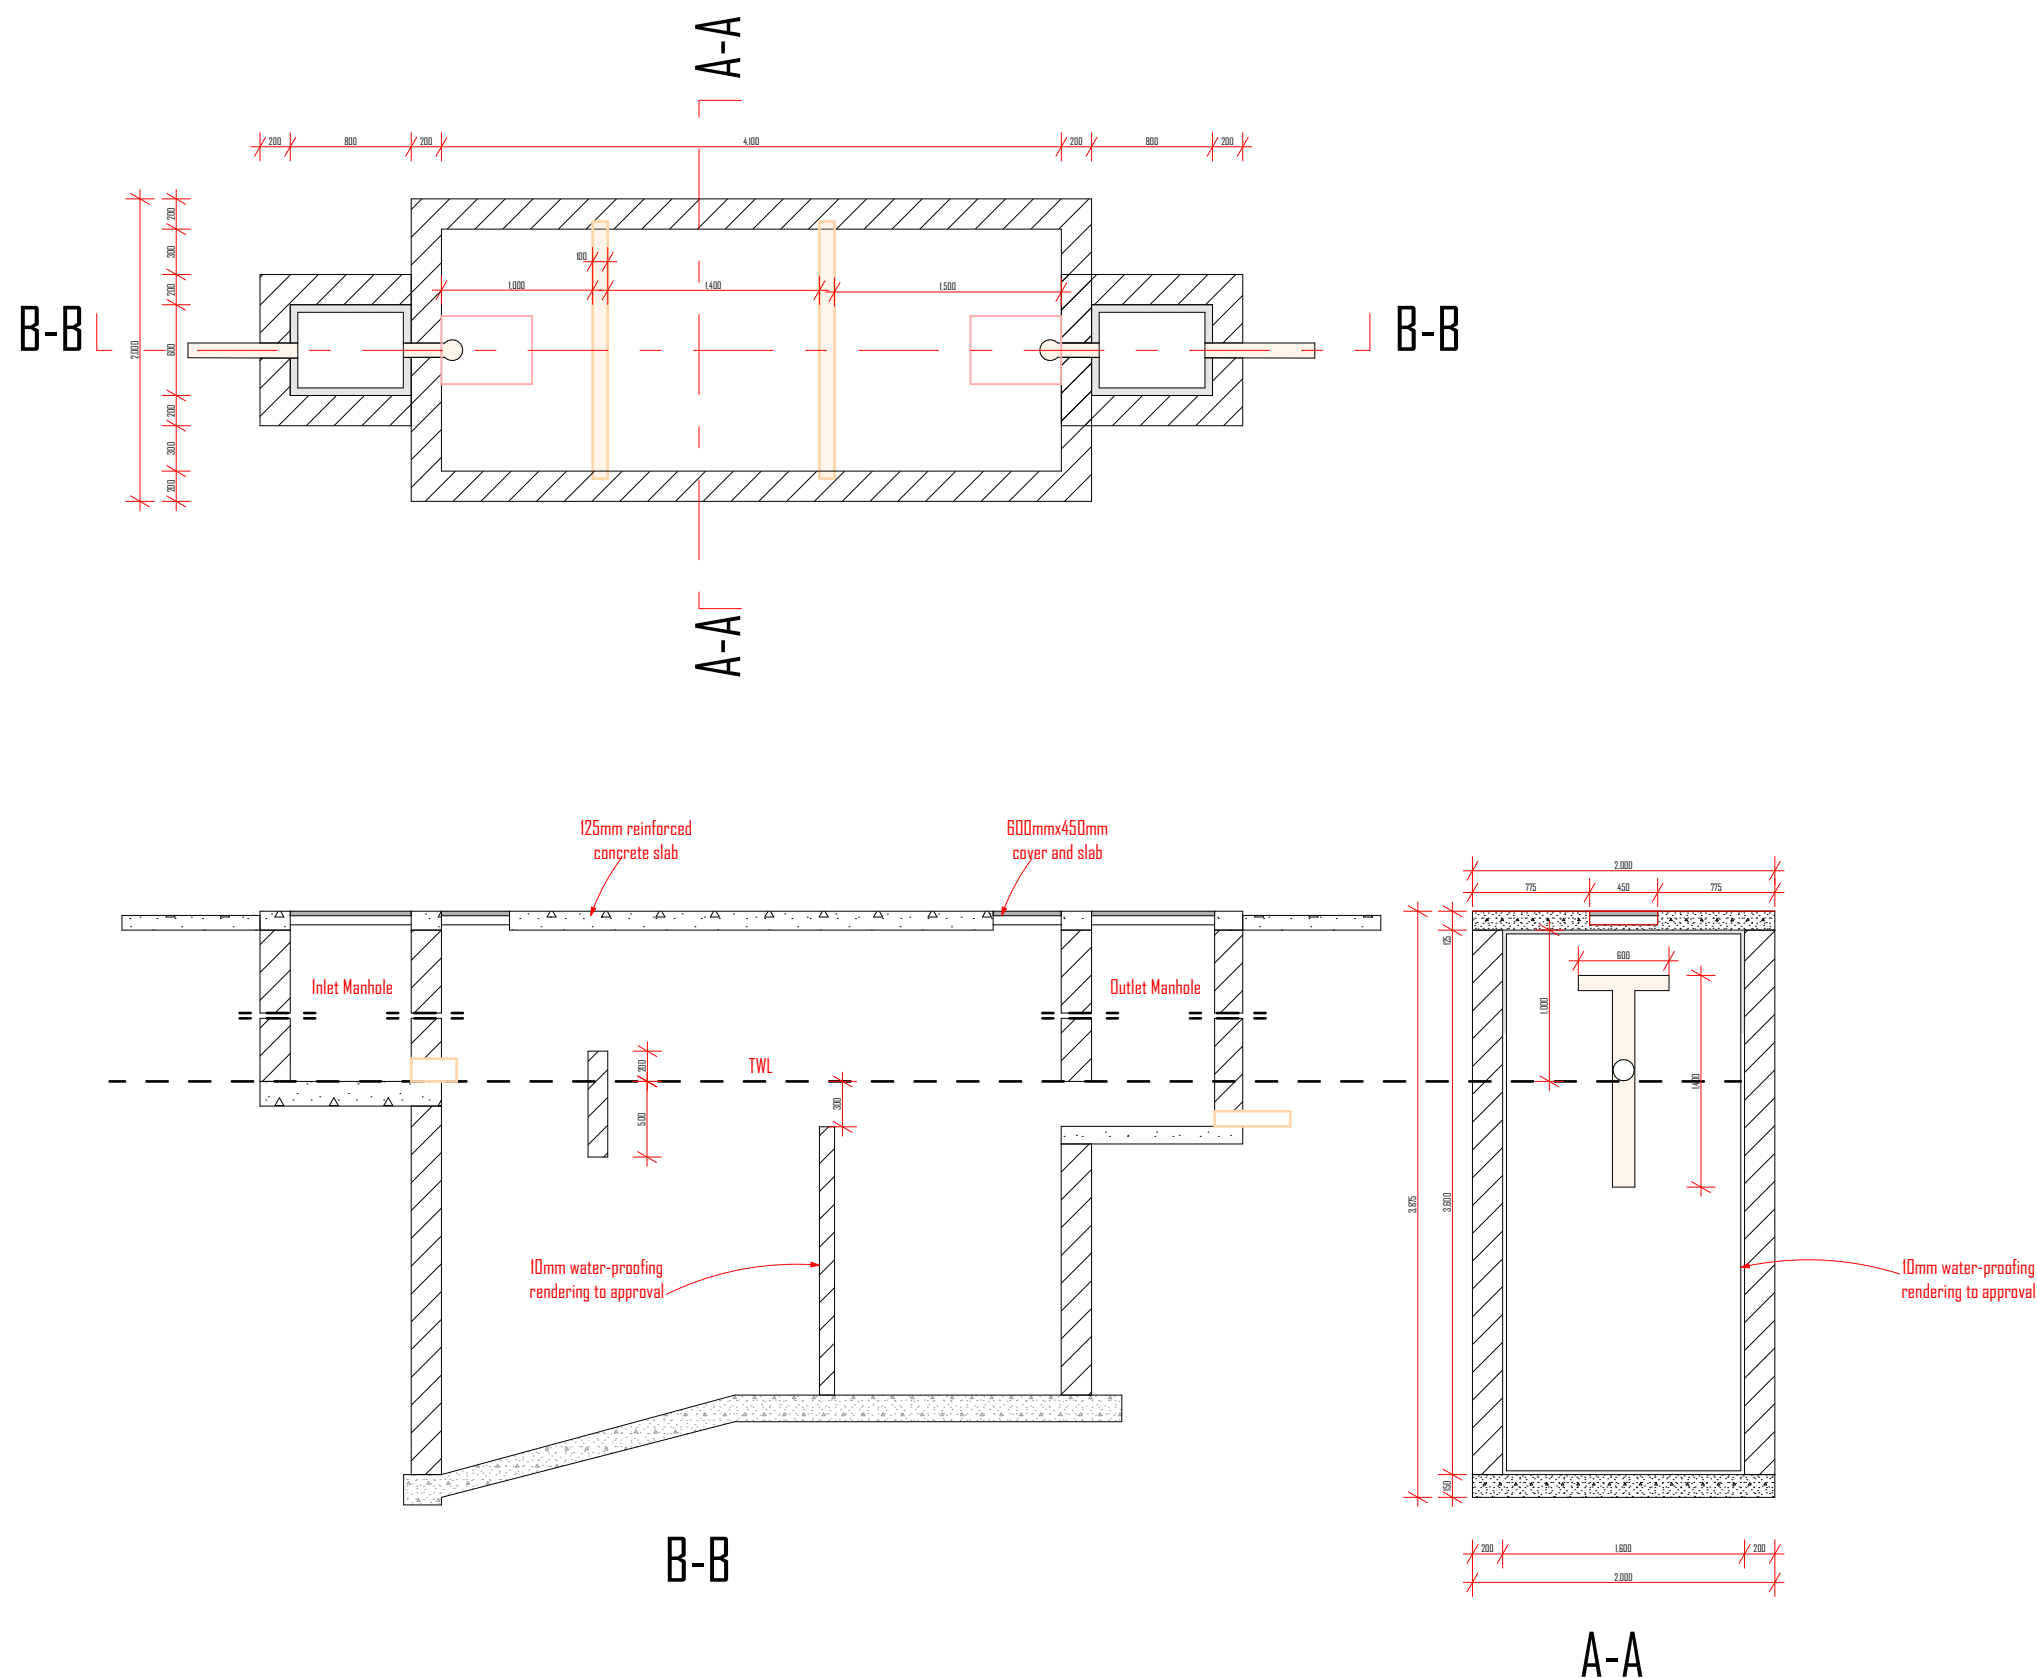

the

KISERIAN HOUSE

NOTES

CLIENT

Ms. Linda Munyendo

Location: Kiserian, Kajiado

Plot Number: Kajiado/ OLCHORO onyore/ 34169

ORIENTATION




SCALE


1:100

Schedules


A3.19

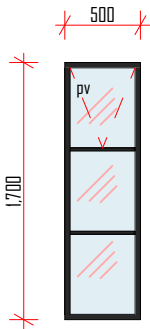


Type	W1
Dimensions	1700mm X 500mm
Sill Height	600mm
Description	Top-hung aluminium-framed window
No.	5 no.

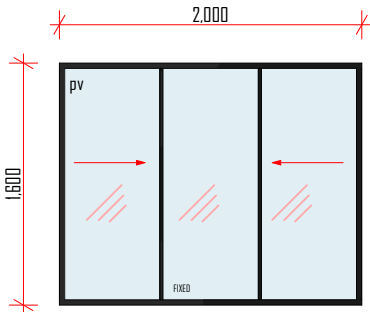


Type	W2
Dimensions	2000mm X 1600mm
Sill Height	500mm
Description	Sliding aluminium-framed window
No.	4 no.

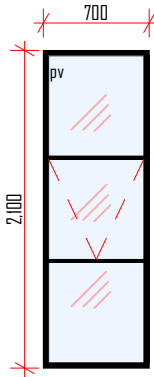


Type	W3
Dimensions	2100mm X 700mm
Sill Height	100mm
Description	Centre-hung aluminium-framed window
No.	2 no.

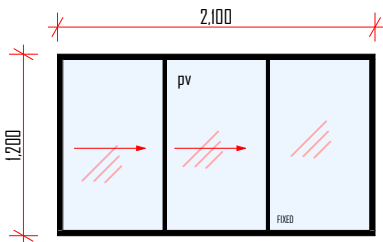

Type	W4
Dimensions	1200mm X 2100mm
Sill Height	1000mm
Description	Sliding aluminium-framed window
No.	1 no.

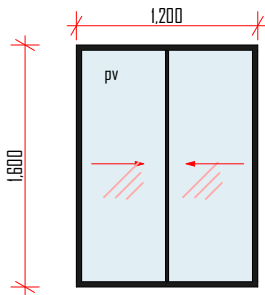

Type	W5
Dimensions	1600mm X 1200mm
Sill Height	600mm
Description	Sliding aluminium-framed window
No.	1 no.

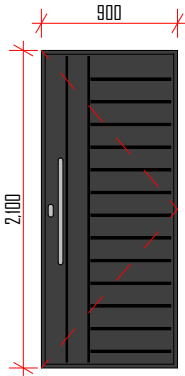

Type	D1
Dimensions	2100mm X 900mm
Sill Height	0mm
Description	Steel single-swing hinged door
No.	2 no.

the **KISERIAN HOUSE**

NOTES

CLIENT

Ms. Linda Munyendo

Location: Kiserian, Kajiado

Plot Number: Kajiado/ OLCHORO onyore/ 34169

ORIENTATION



SCALE

1:100

Renders

A3.20





the **KISERIAN HOUSE**

NOTES

CLIENT
Ms. Linda Munyendo

Location: Kiserian, Kajiado

Plot Number: Kajiado/ OLCHORO onyore/ 34169

ORIENTATION



SCALE 1:100

Renders

A3.21



the **KISERIAN HOUSE**

NOTES

CLIENT

Ms. Linda Munyendo

Location: Kiserian, Kajjado

Plot Number: Kajjado/ OLCHORO onyore/ 34169

ORIENTATION



SCALE

1:100

Renders

A3.22

the **KISERIAN HOUSE**

NOTES

CLIENT

Ms. Linda Munyendo

Location: Kiserian, Kajiado

Plot Number: Kajiado/ OLCHORO onyore/ 34169

ORIENTATION



SCALE

1:100

Renders

A3.23





the **KISERIAN HOUSE**

NOTES

CLIENT
Ms. Linda Munyendo

Location: Kiserian, Kajiado

Plot Number: Kajiado/ OLCHORO onyore/ 34169


ORIENTATION



SCALE 1:100

Renders

A3.24

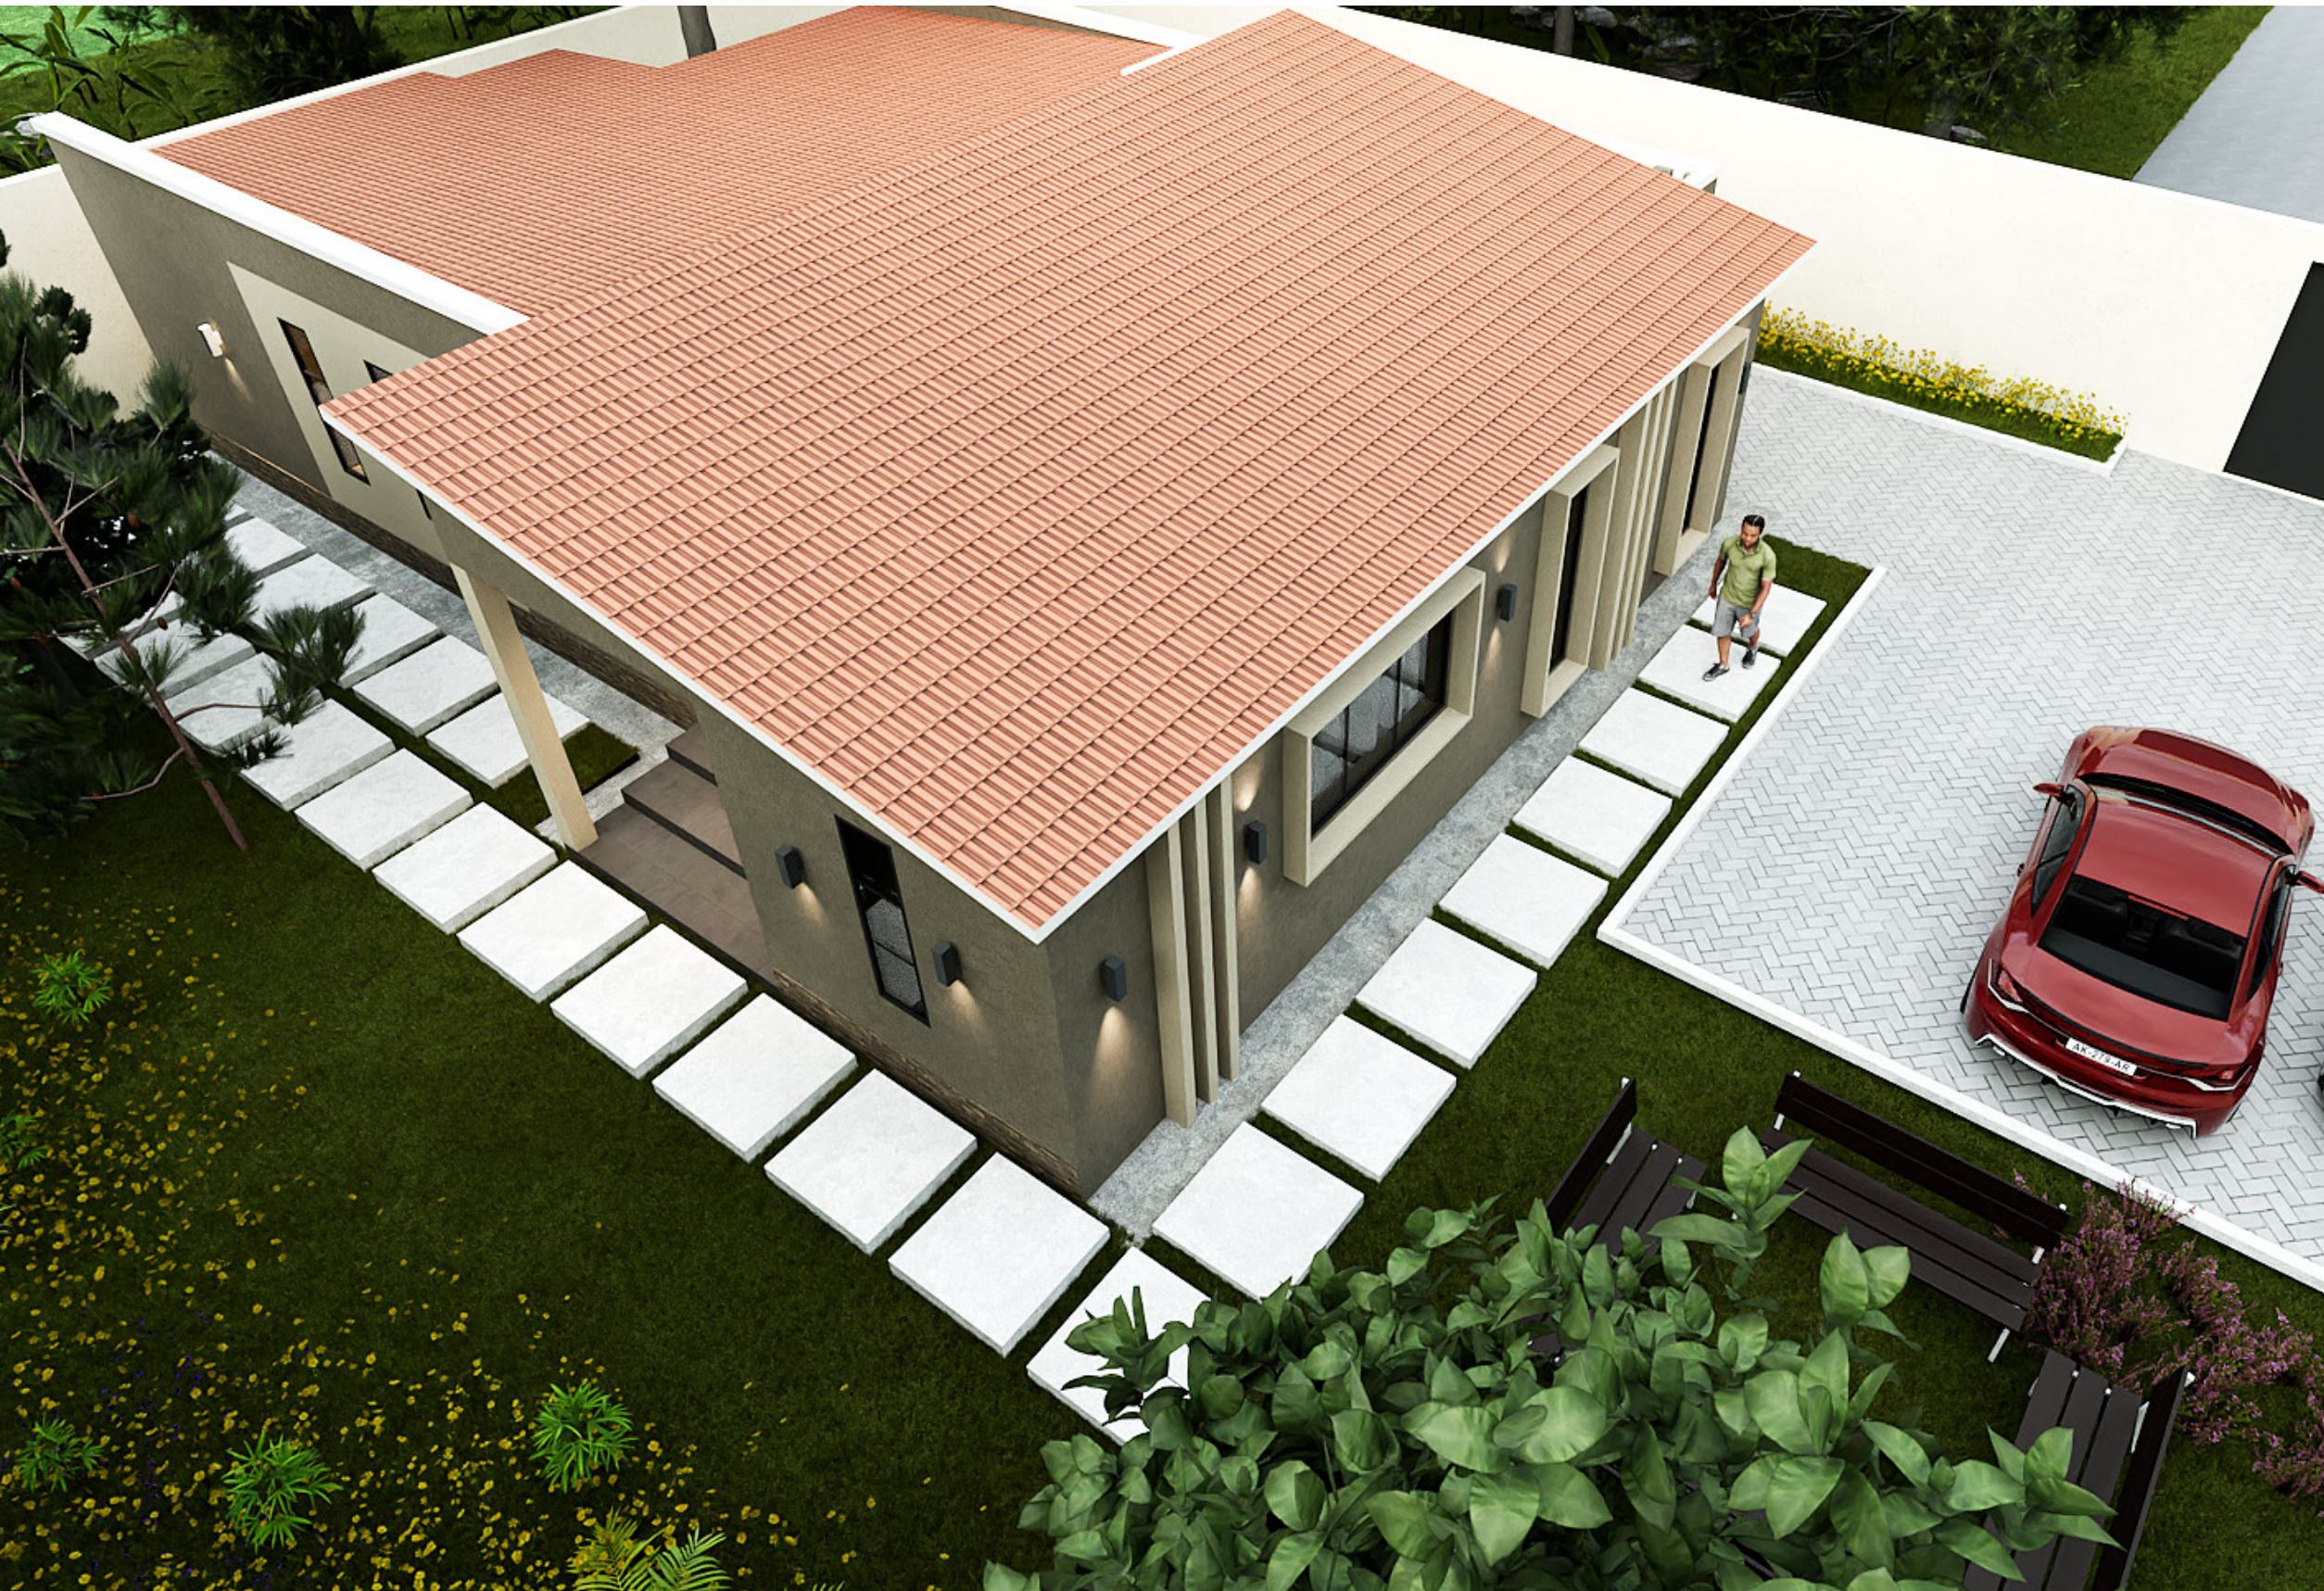

the **KISERIAN HOUSE**

NOTES


CLIENT

Ms. Linda Munyendo

Location: Kiserian, Kajiado

Plot Number: Kajiado/ OLCHORO onyore/ 34169

ORIENTATION

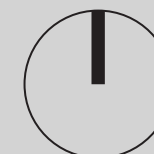

SCALE

1:100

Renders

A3.25

the **KISERIAN HOUSE**

NOTES

CLIENT
Ms. Linda Munyendo

Location: Kiserian, Kajiado

Plot Number: Kajiado/ OLCHORO onyore/ 34169


ORIENTATION



SCALE 1:65

Interior Ceiling Plan

A3.26

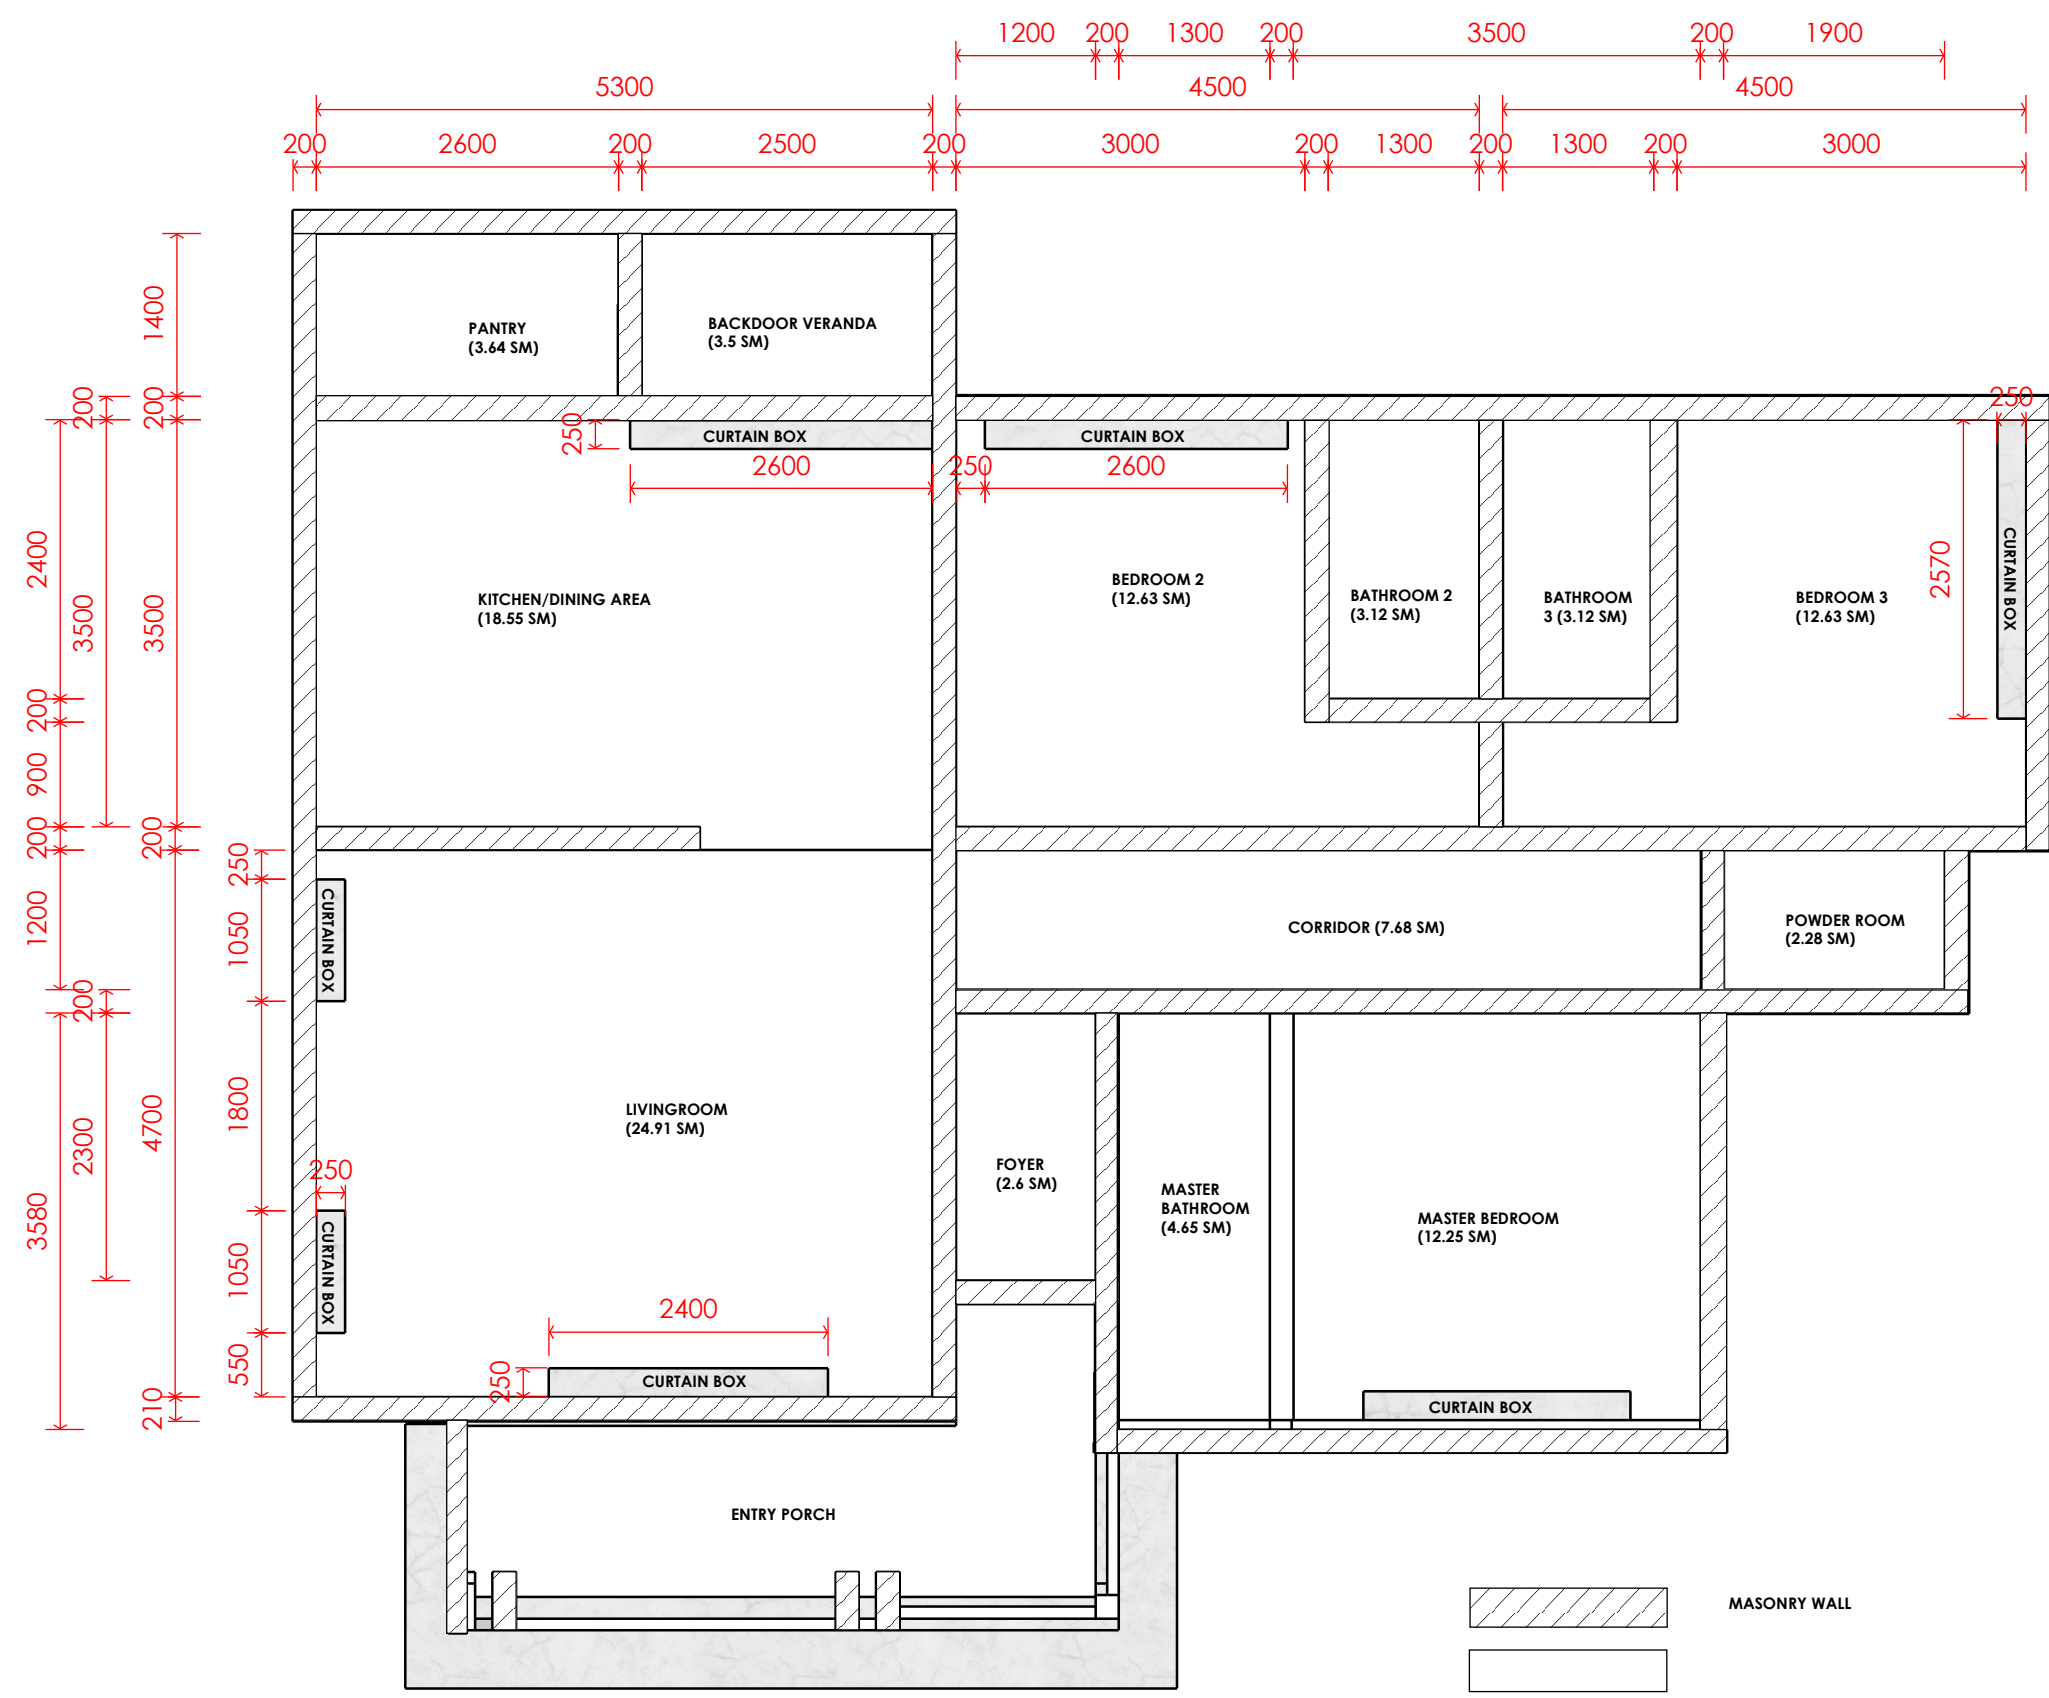

CEILING PLAN

the **KISERIAN HOUSE**

NOTES

CLIENT

Ms. Linda Munyendo

Location: Kiserian, Kajiado

Plot Number: Kajiado/ OLCHORO onyore/ 34169

ORIENTATION




SCALE

1:65

Flooring Plan

A3.27

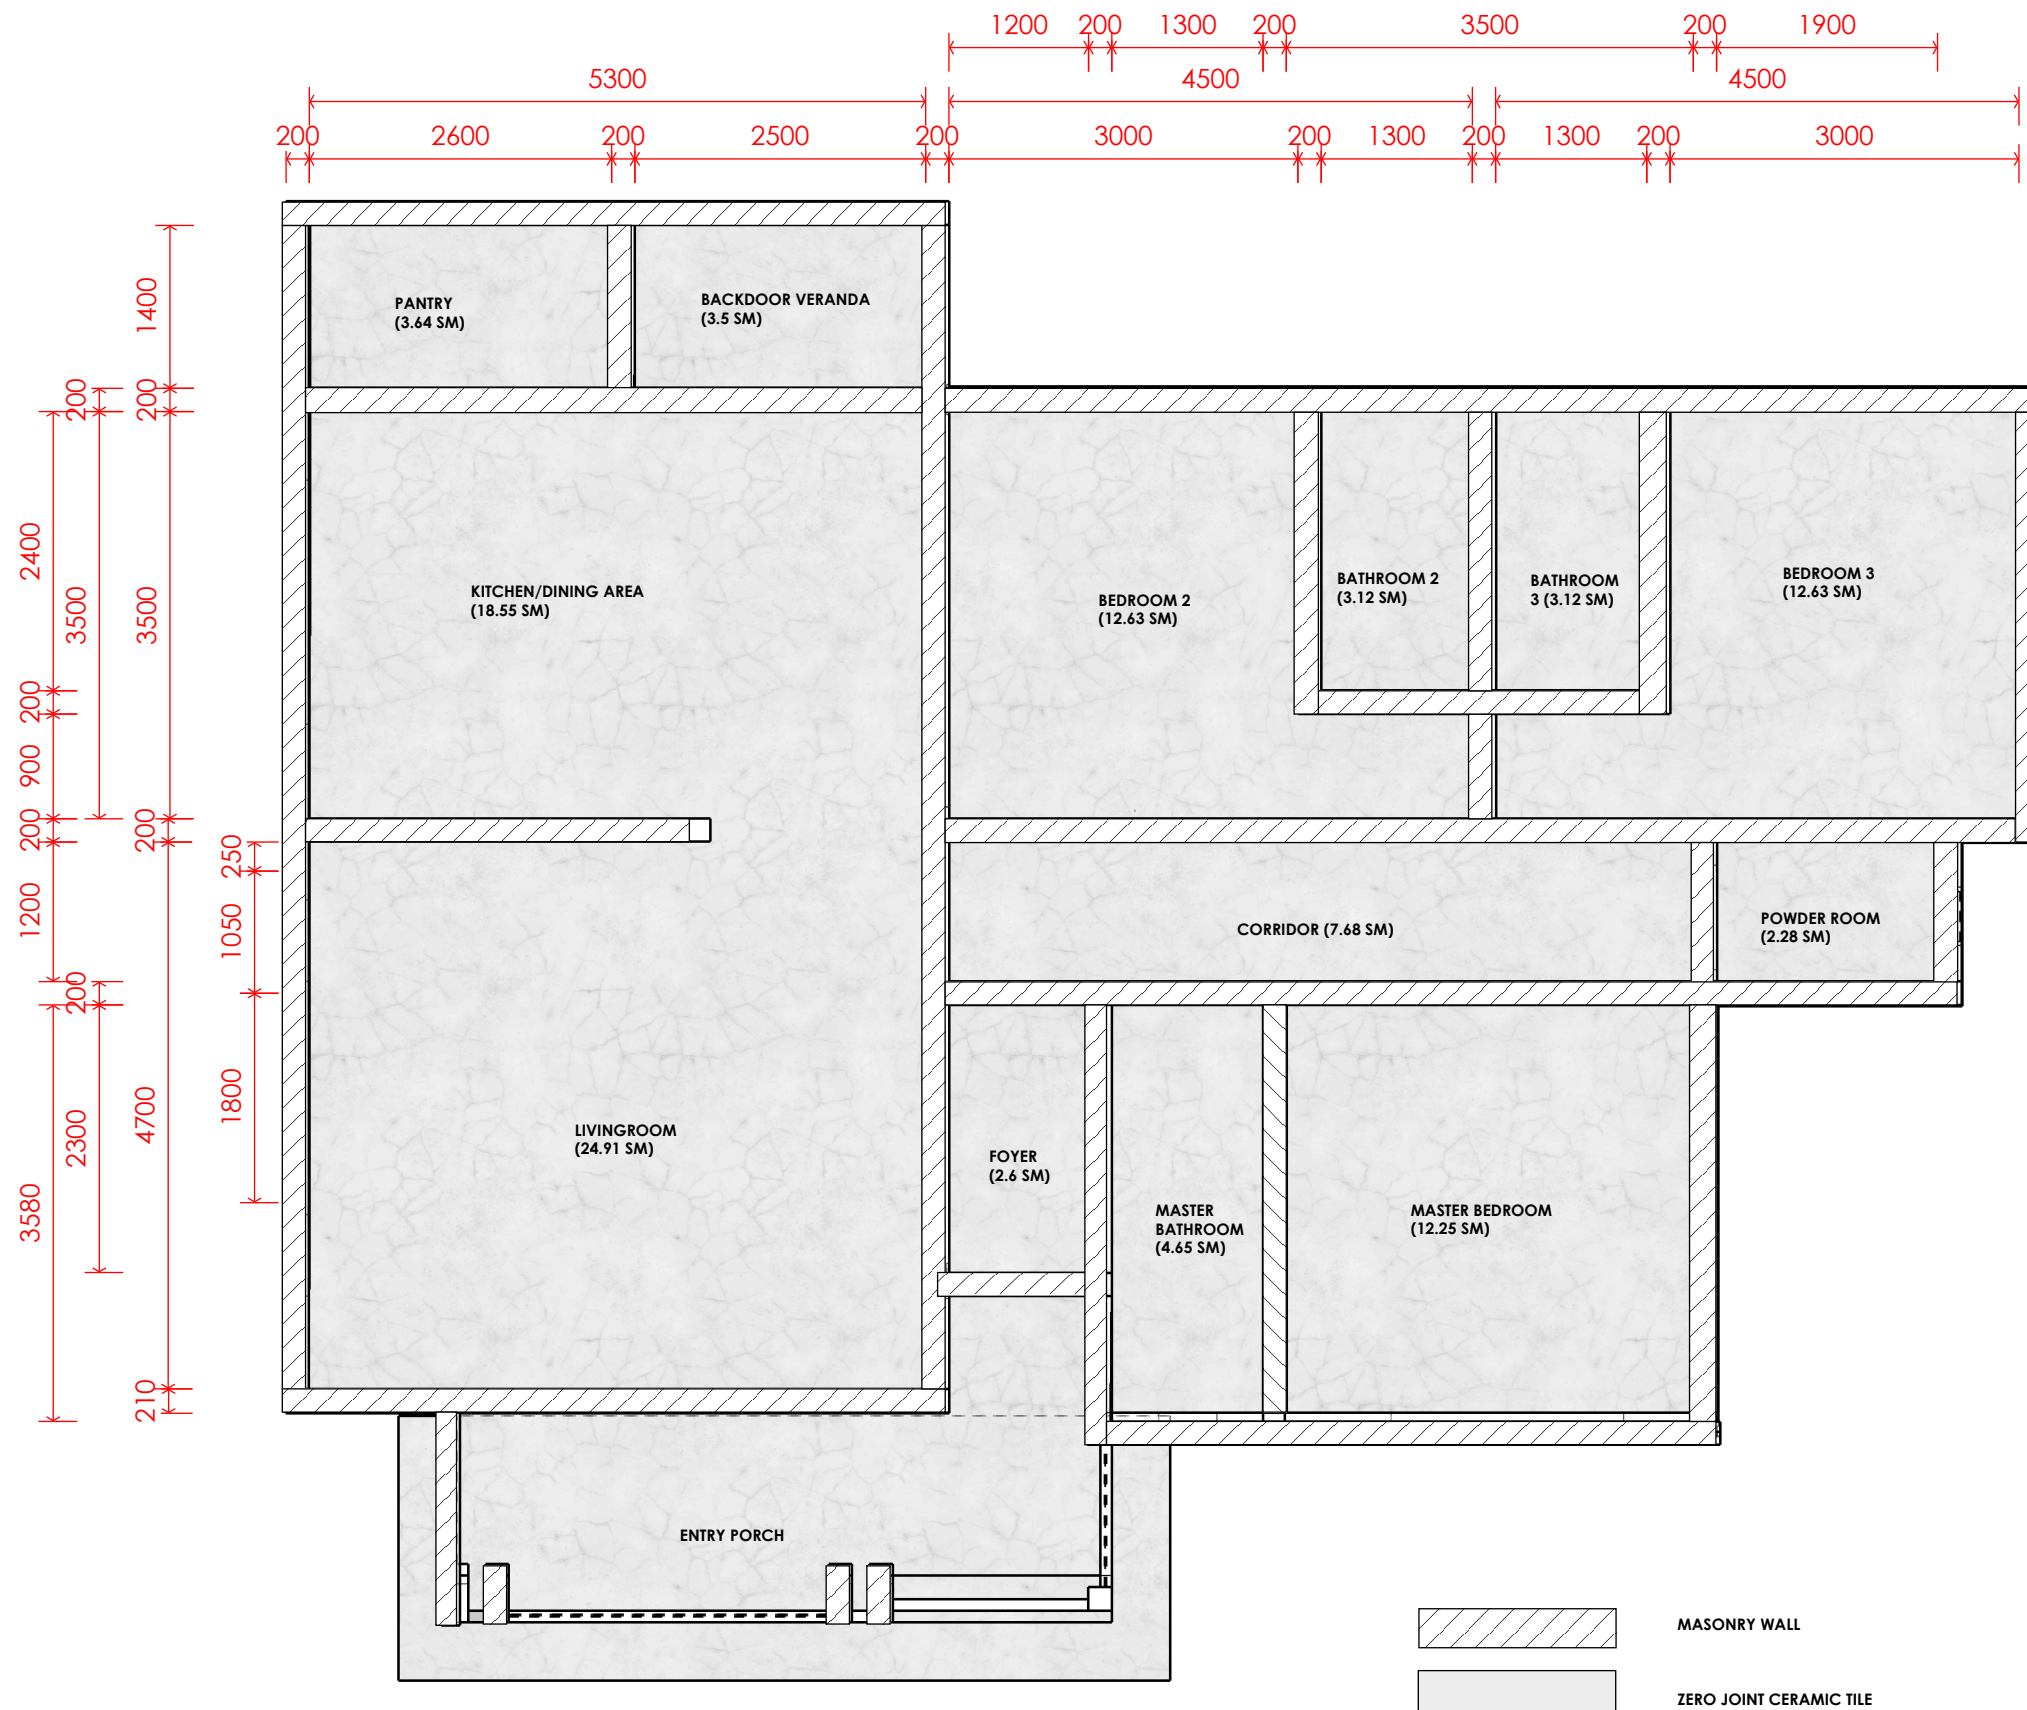

FLOORING PLAN

the **KISERIAN HOUSE**


NOTES

CLIENT
Ms. Linda Munyendo
Location: Kiserian, Kajiado
Plot Number: Kajiado/ OLCHORO onyore/ 34169

ORIENTATION



SCALE 1:65

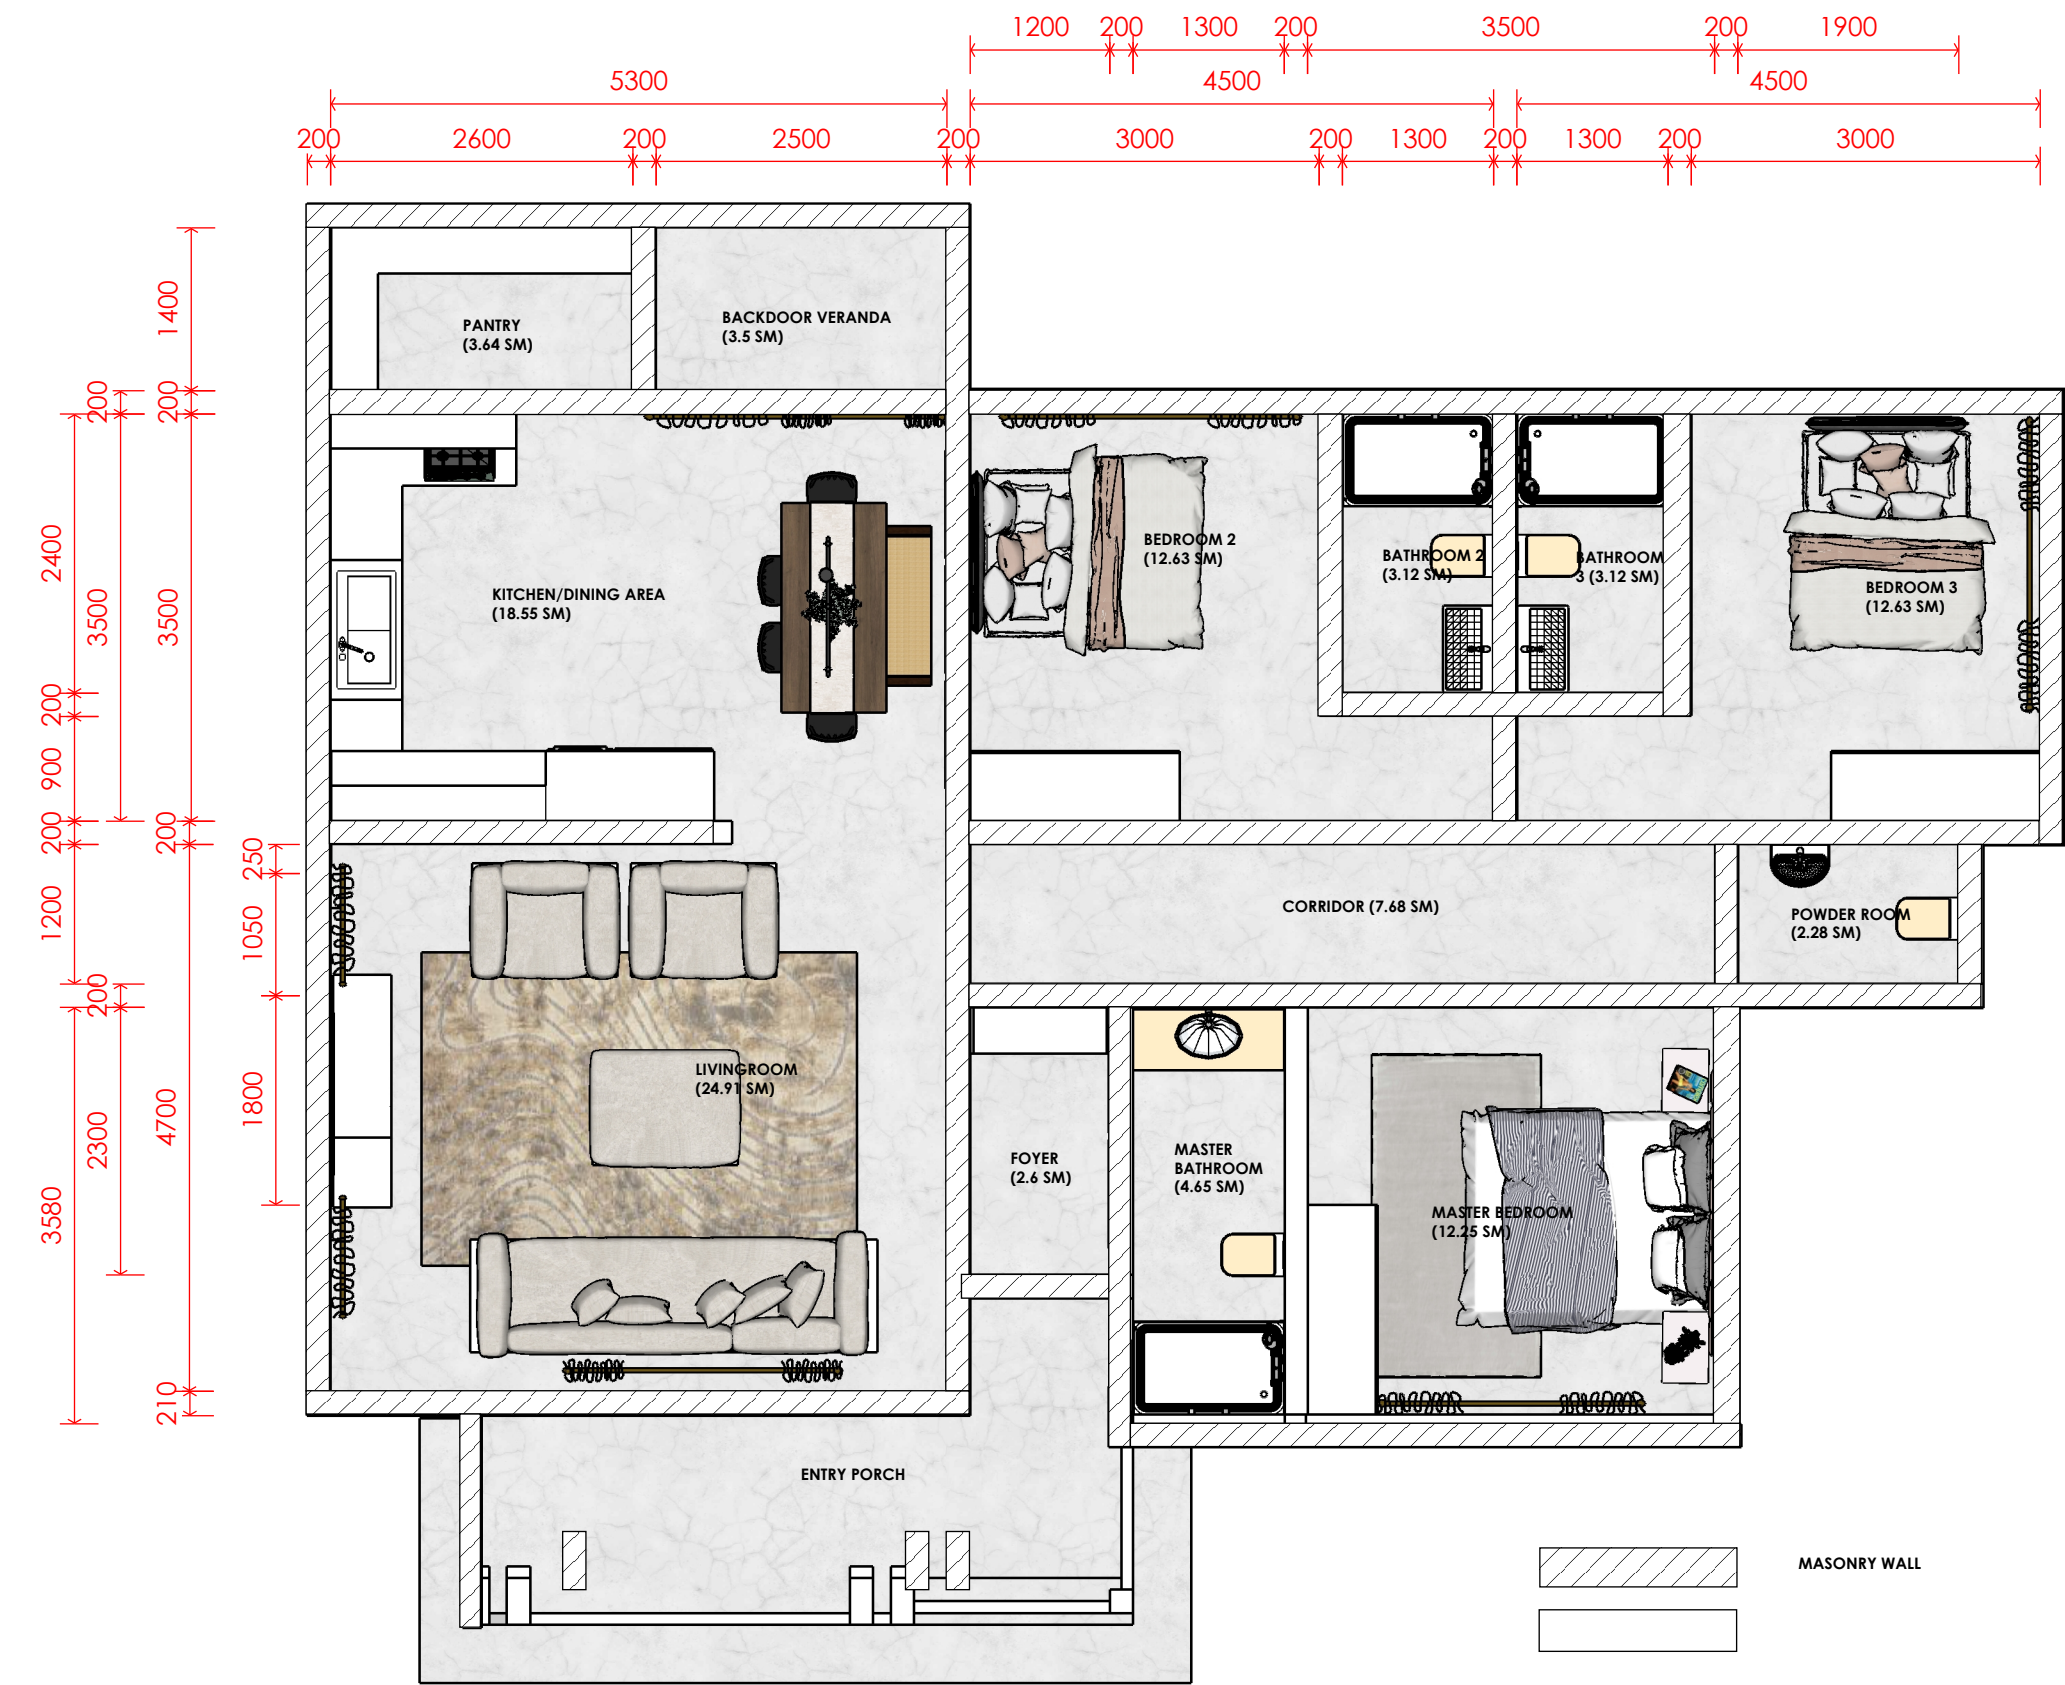

FURNITURE PLAN

the **KISERIAN HOUSE**

NOTES

CLIENT

Ms. Linda Munyendo

Location: Kiserian, Kajiado

Plot Number: Kajiado/ OLCHORO onyore/ 34169

ORIENTATION




SCALE

1:65

Reflected Ceiling Plan

A3.29

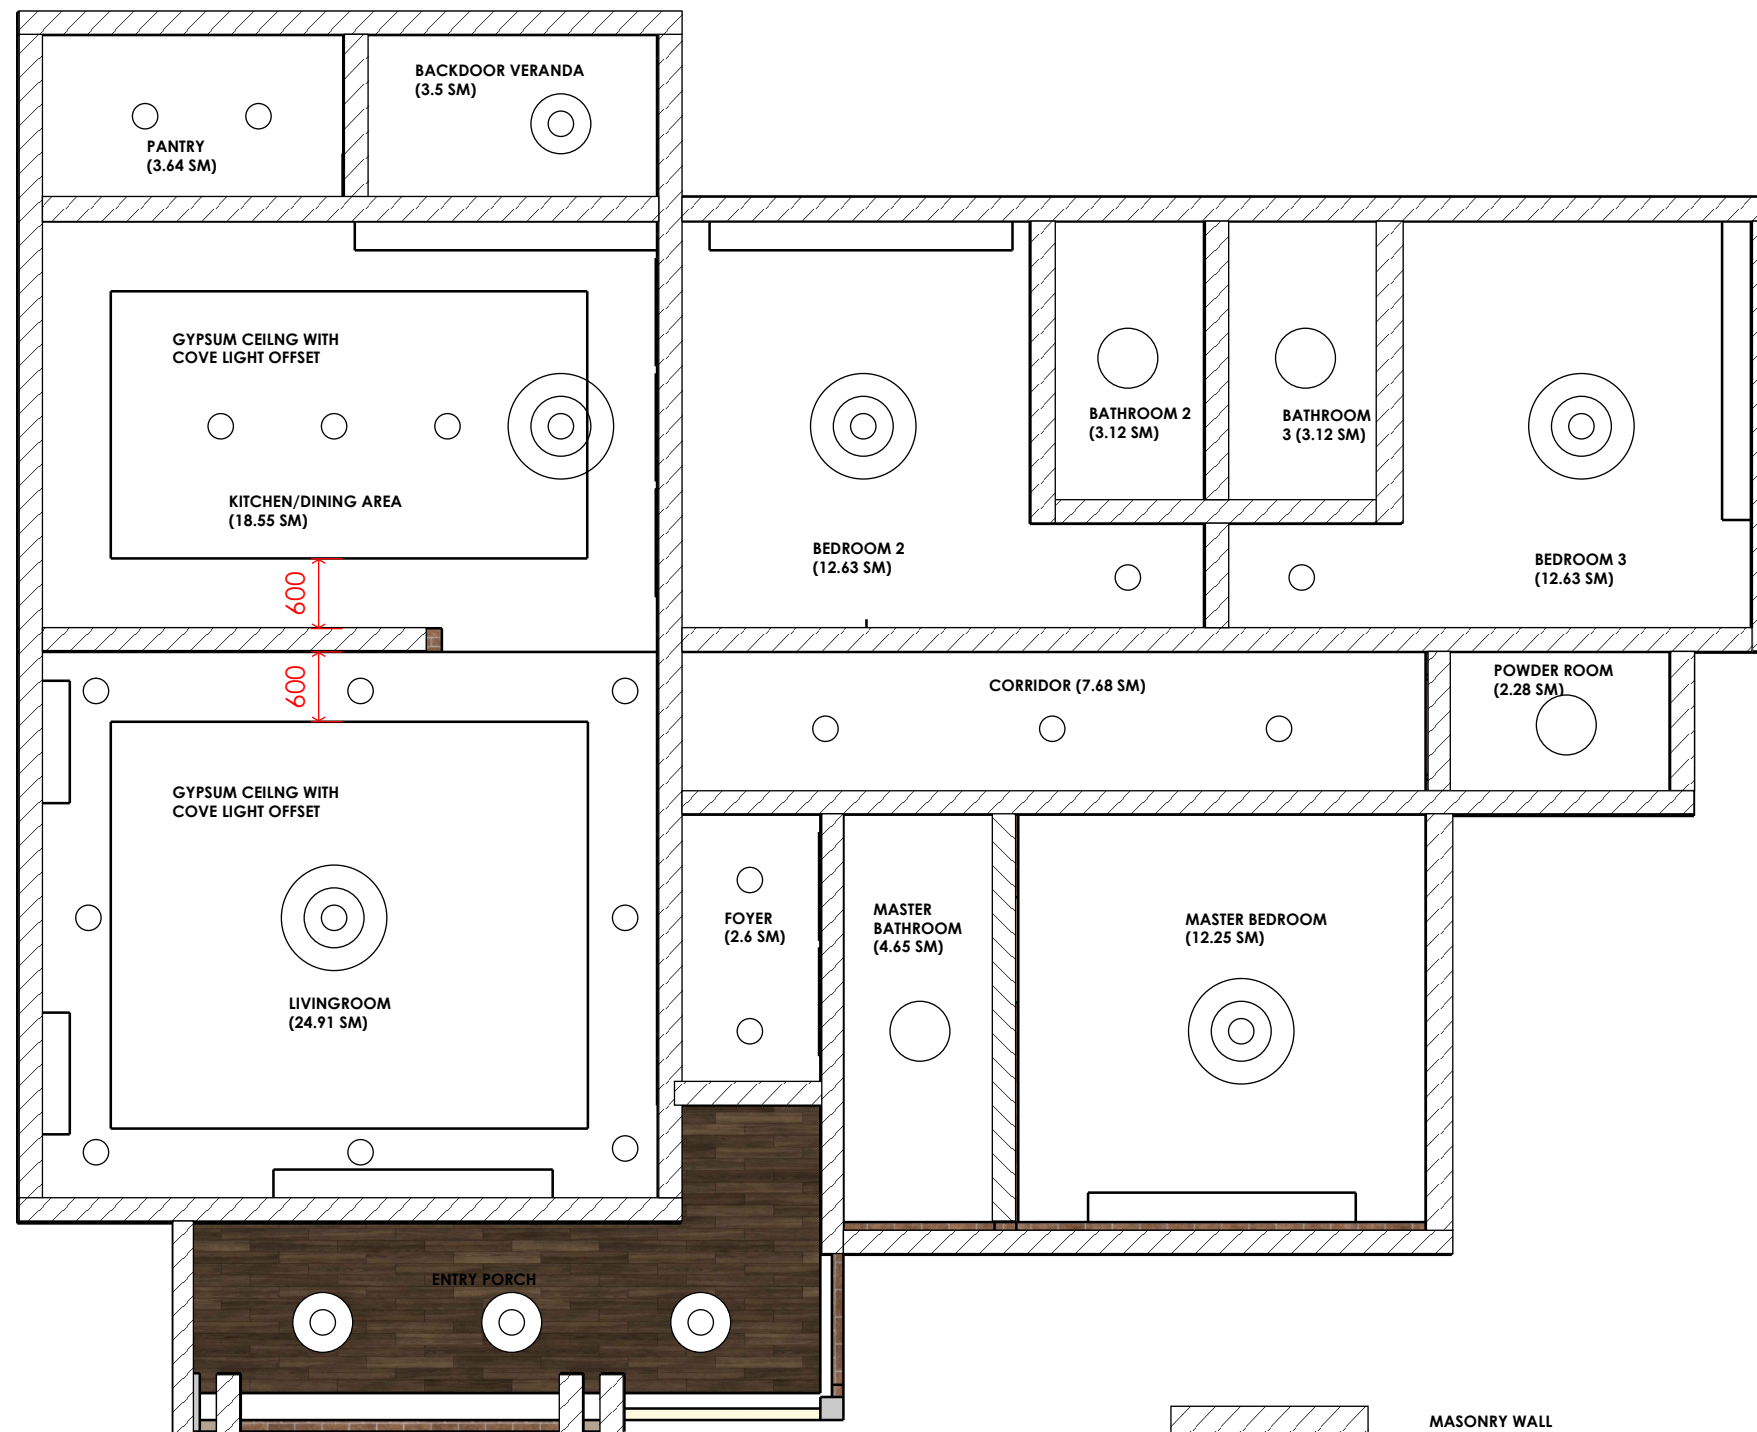

REFLECTED CEILING PLAN

MASONRY WALL

DECORATIVE CENTER LIGHT
TO CLIENT'S PREFERENCE

EXTERIOR LIGHTS
TO CLIENT'S PREFERENCE

BATHROOM LIGHTS TO
CLIENT'S PREFERENCE

WARM WHITE DOWN LIGHTS

the **KISERIAN HOUSE**

NOTES

CLIENT
Ms. Linda Munyendo

Location: Kiserian, Kajiado

Plot Number: Kajiado/ OLCHORO onyore/ 34169


ORIENTATION




SCALE 1:65

Lighting Plan


A3.30

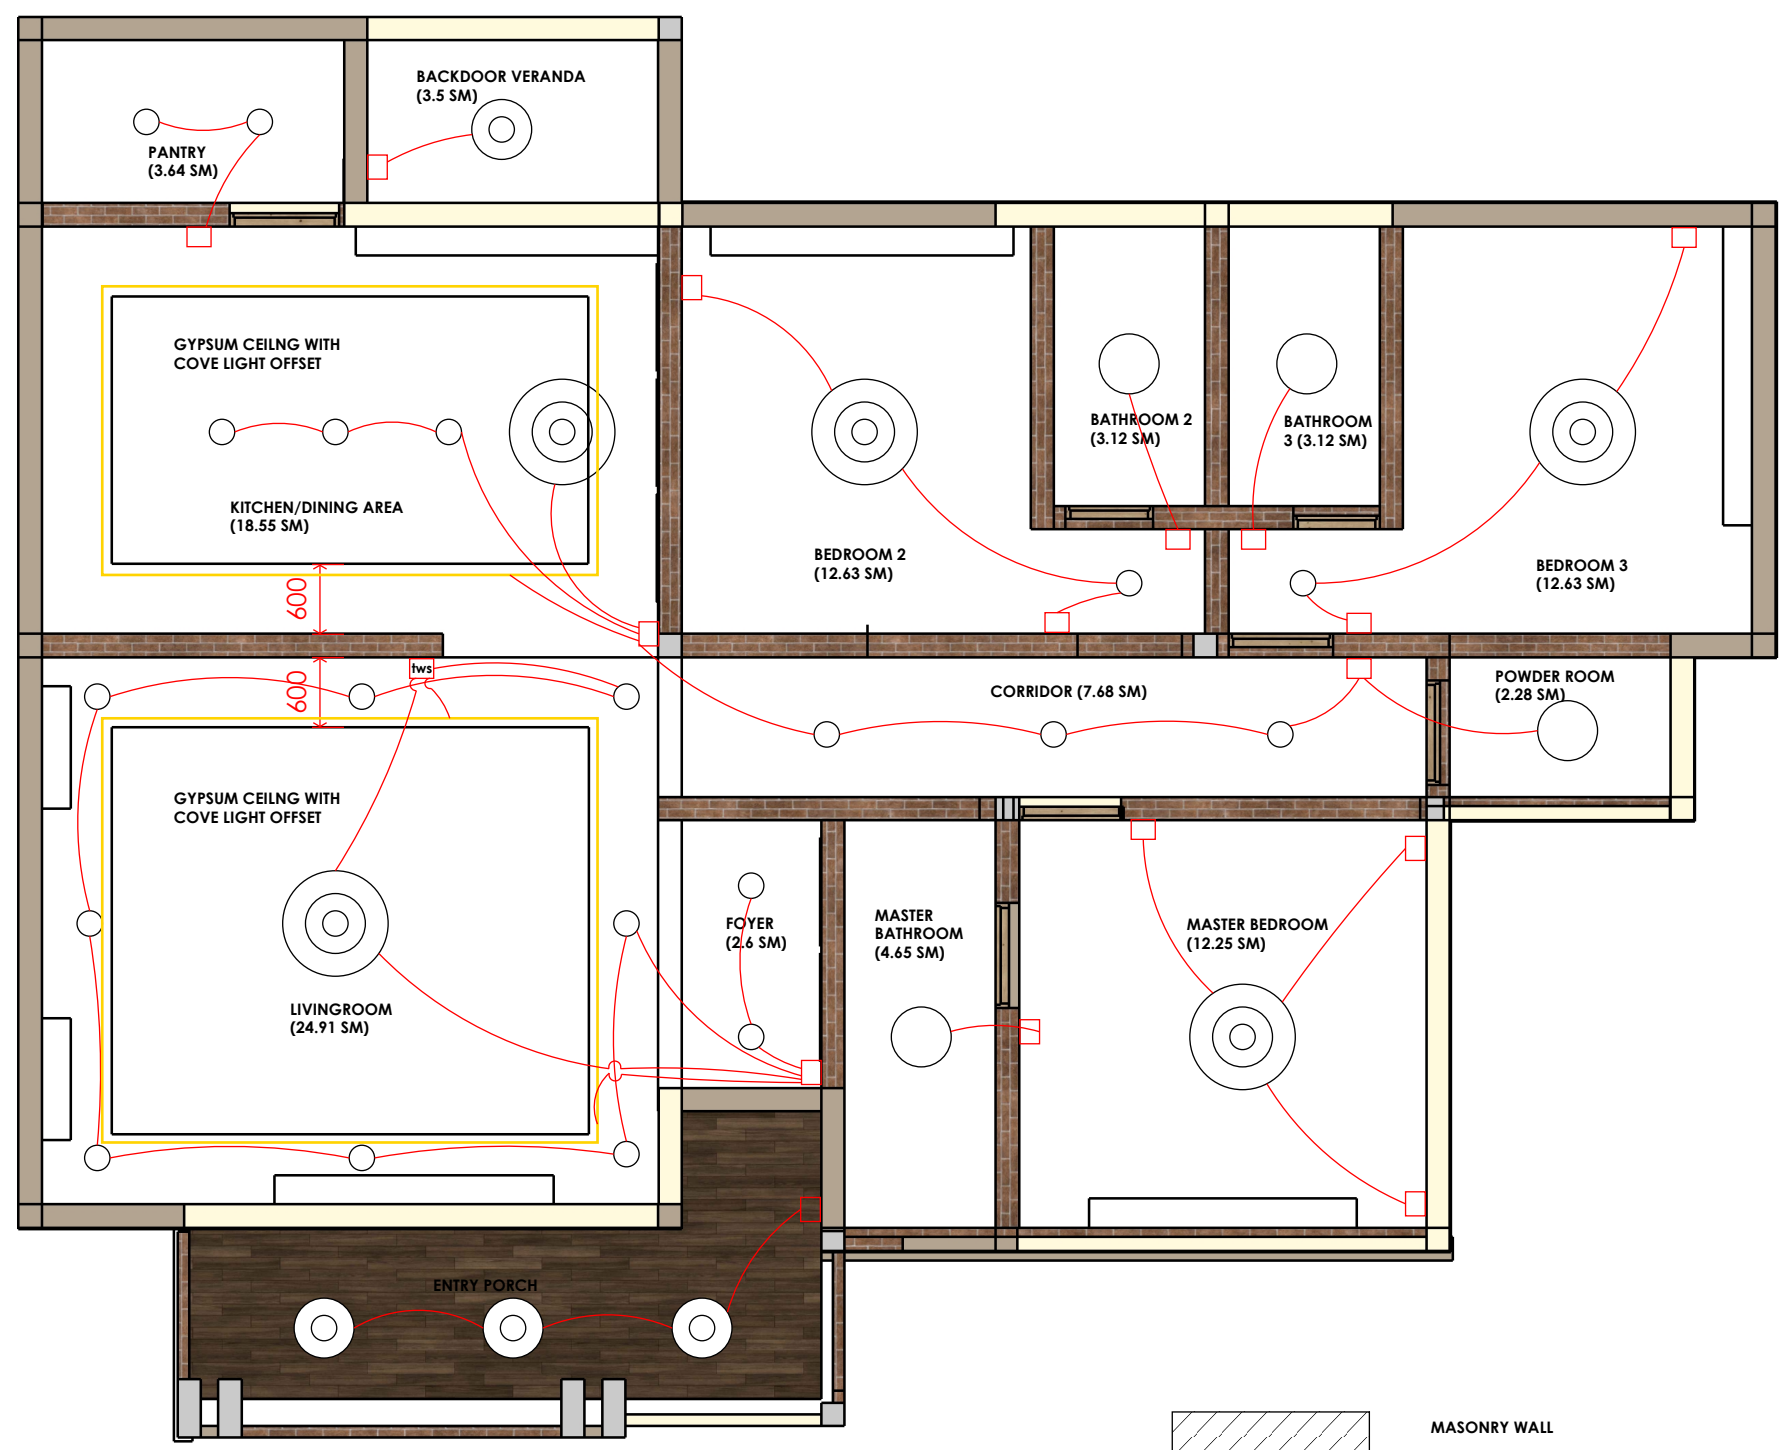

LIGHTING PLAN

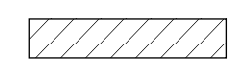

MASONRY WALL

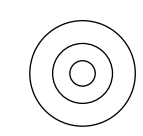

DECORATIVE CENTER LIGHT
TO CLIENT'S PREFERENCE



BATHROOM LIGHTS TO
CLIENT'S PREFERENCE



WARM WHITE DOWN LIGHTS



EXTERIOR LIGHTS
TO CLIENT'S PREFERENCE



Light Switch (Number of
outlets represent gang)

the KISERIAN HOUSE

NOTES


CLIENT

Ms. Linda Munyendo

Location: Kiserian, Kajiado

Plot Number: Kajiado/ OLCHORO onyore/ 34169

ORIENTATION



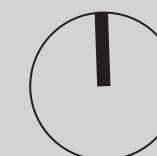


SCALE

1:65

Kitchen Cabinet Drawings

A3.31

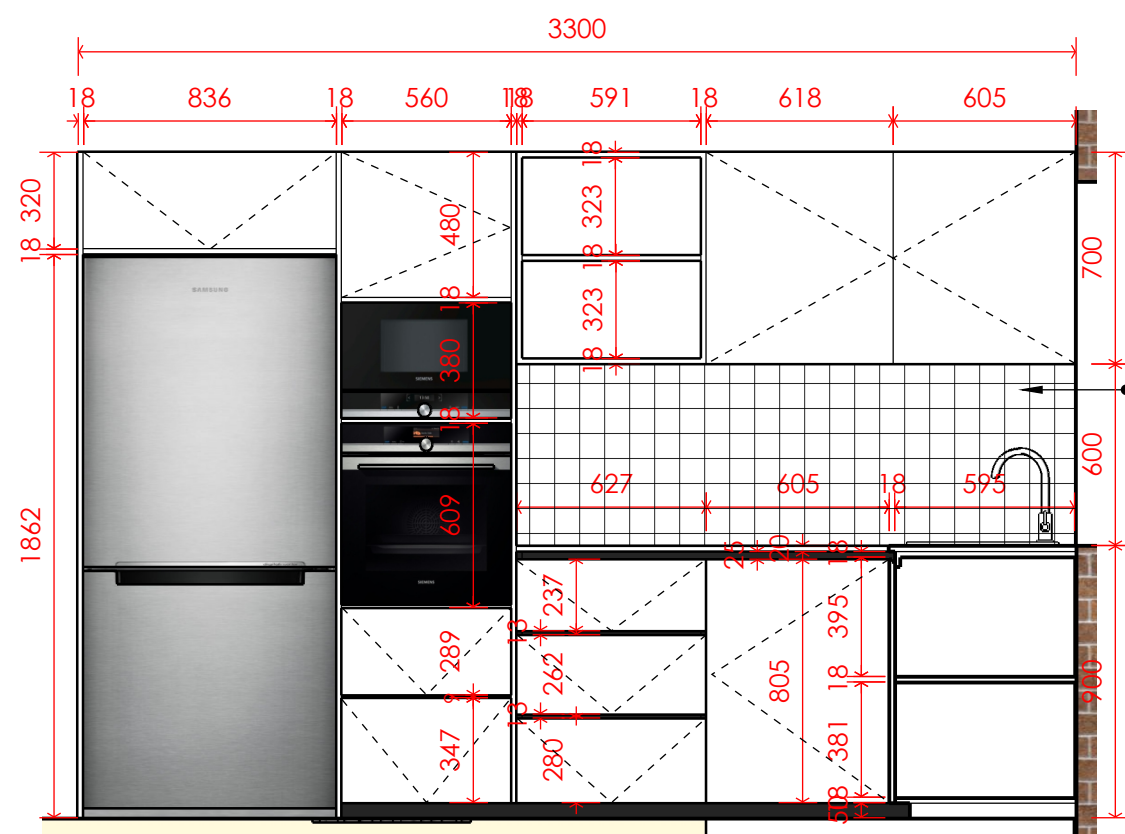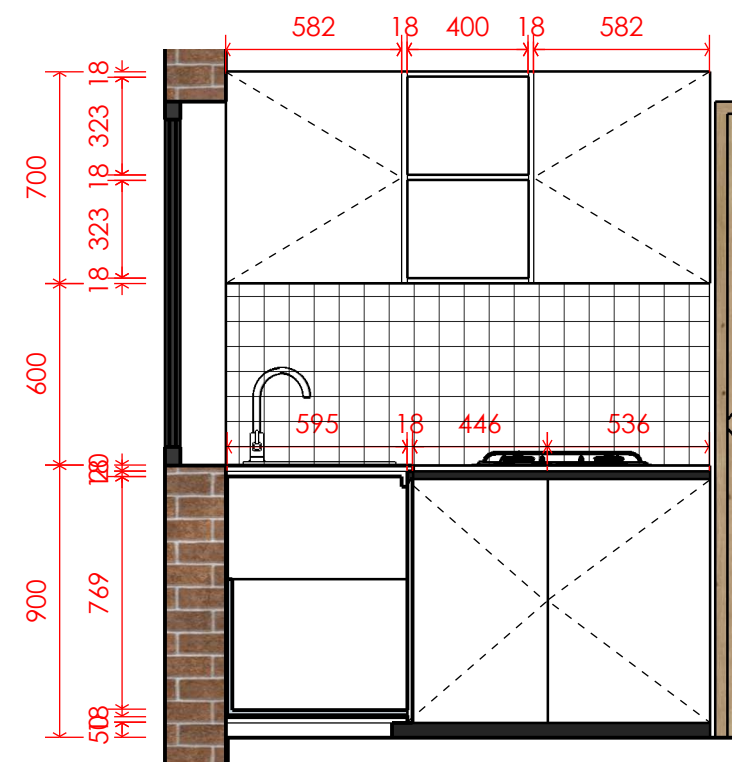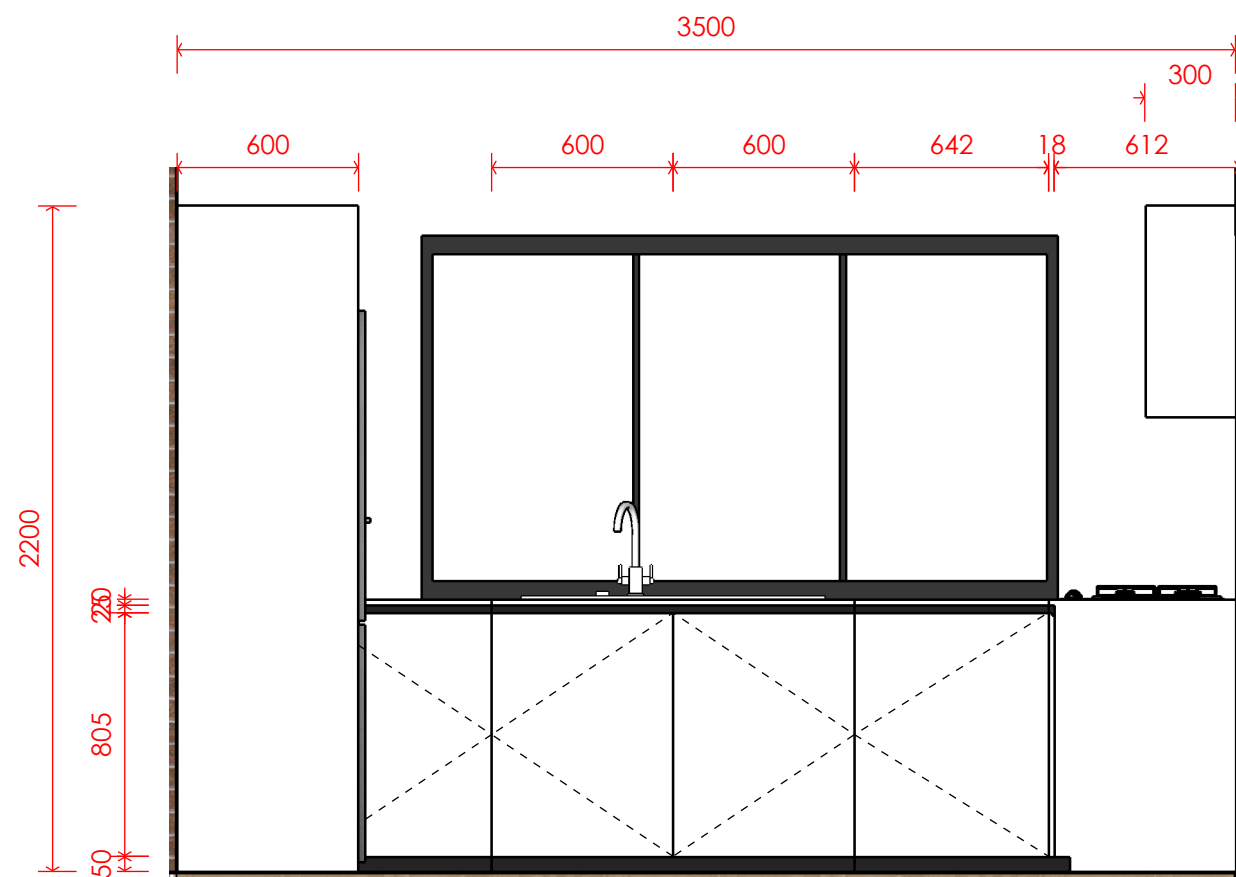

- White Backsplash tile, ceramic brick pattern to client's selection

KITCHEN CABINETS DRAWING

the **KISERIAN HOUSE**

NOTES

CLIENT

Ms. Linda Munyendo

Location: Kiserian, Kajiado

Plot Number: Kajiado/ OLCHORO onyore/ 34169

ORIENTATION




SCALE

1:65

Master Bedroom
Wardrobe drawings

A3.32

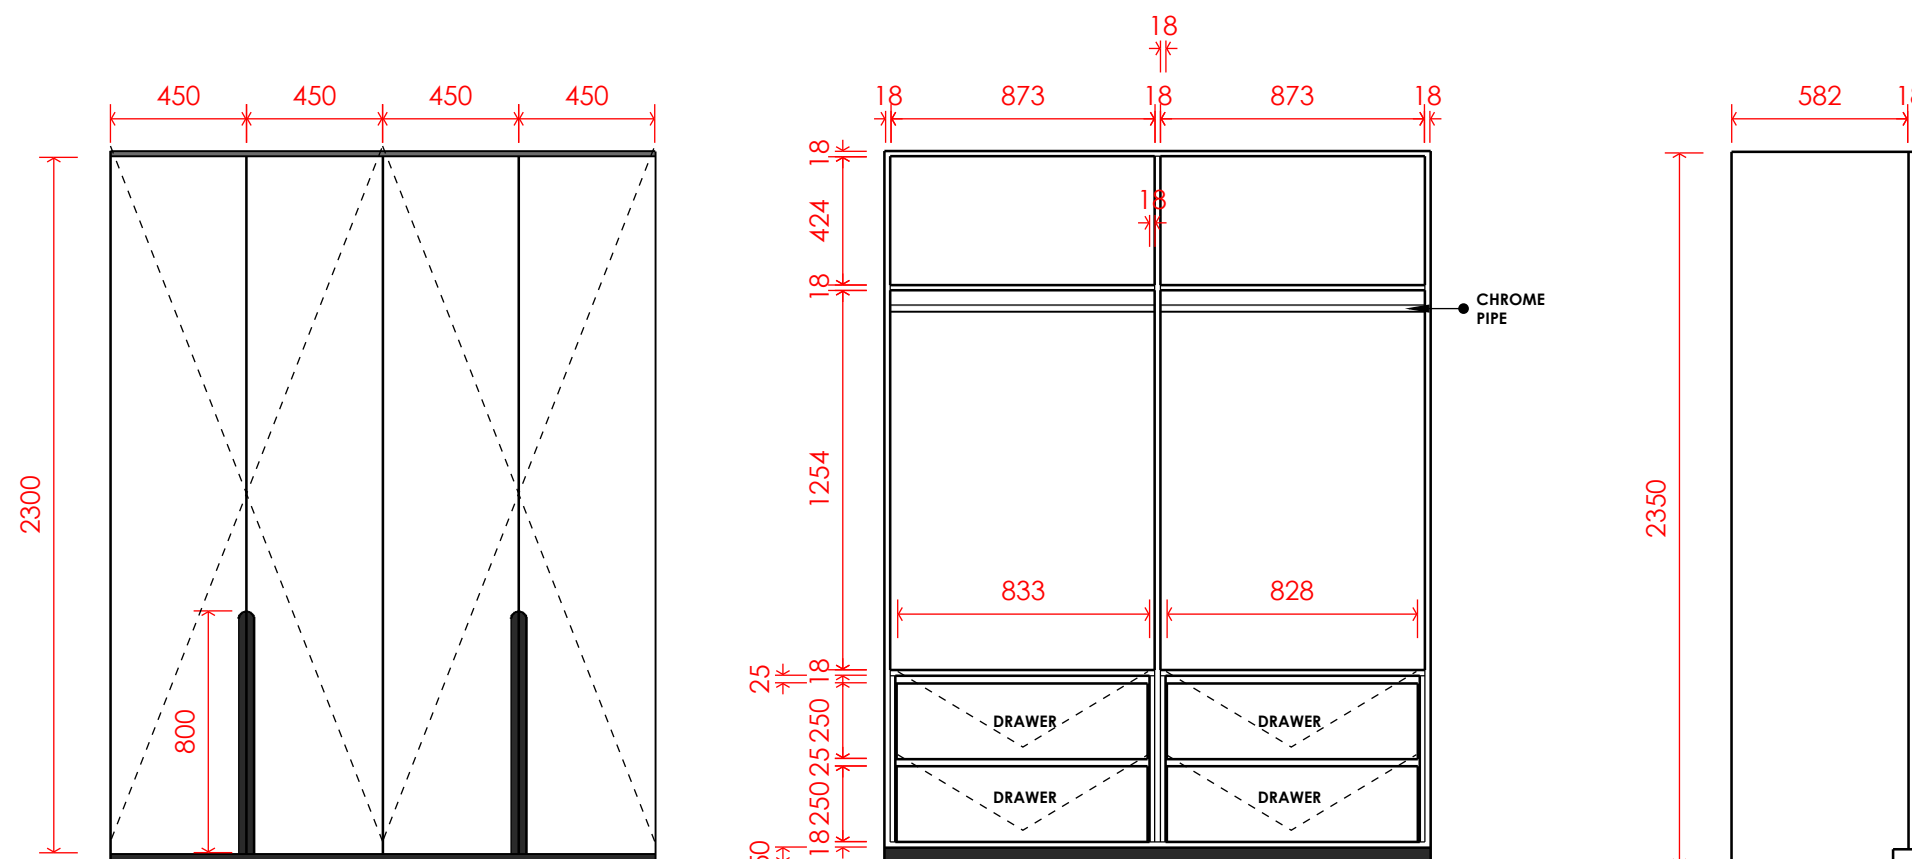

the **KISERIAN HOUSE**

NOTES

CLIENT

Ms. Linda Munyendo

Location: Kiserian, Kajiado

Plot Number: Kajiado/ OLCHORO onyore/ 34169

ORIENTATION





SCALE

1:65

Bedroom 01 & 02
Wardrobe drawings

A3.33

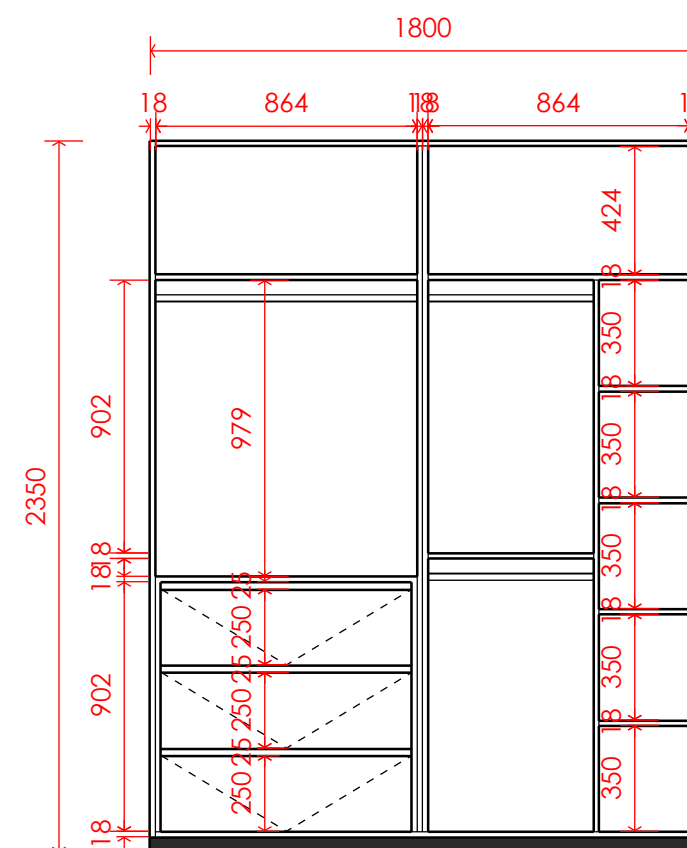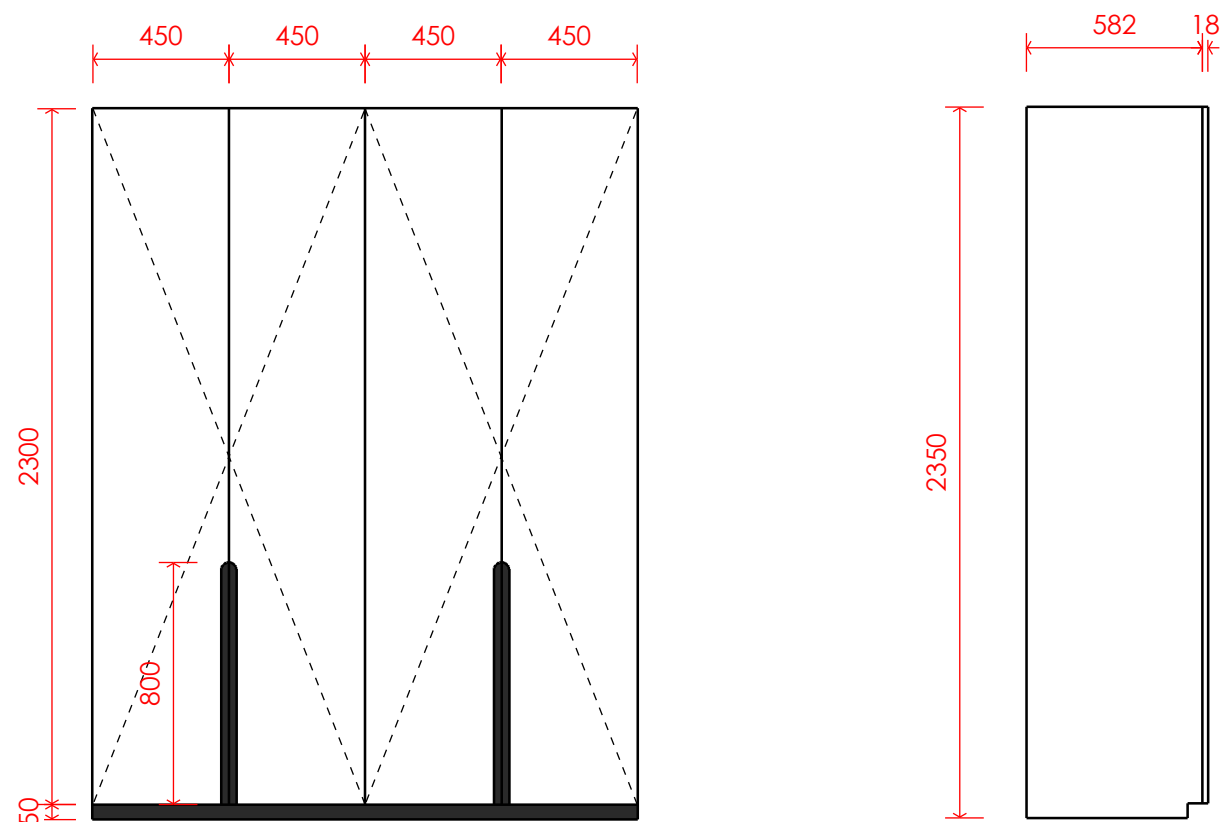

BEDROOM 1&2 WARDROBE DRAWINGS